


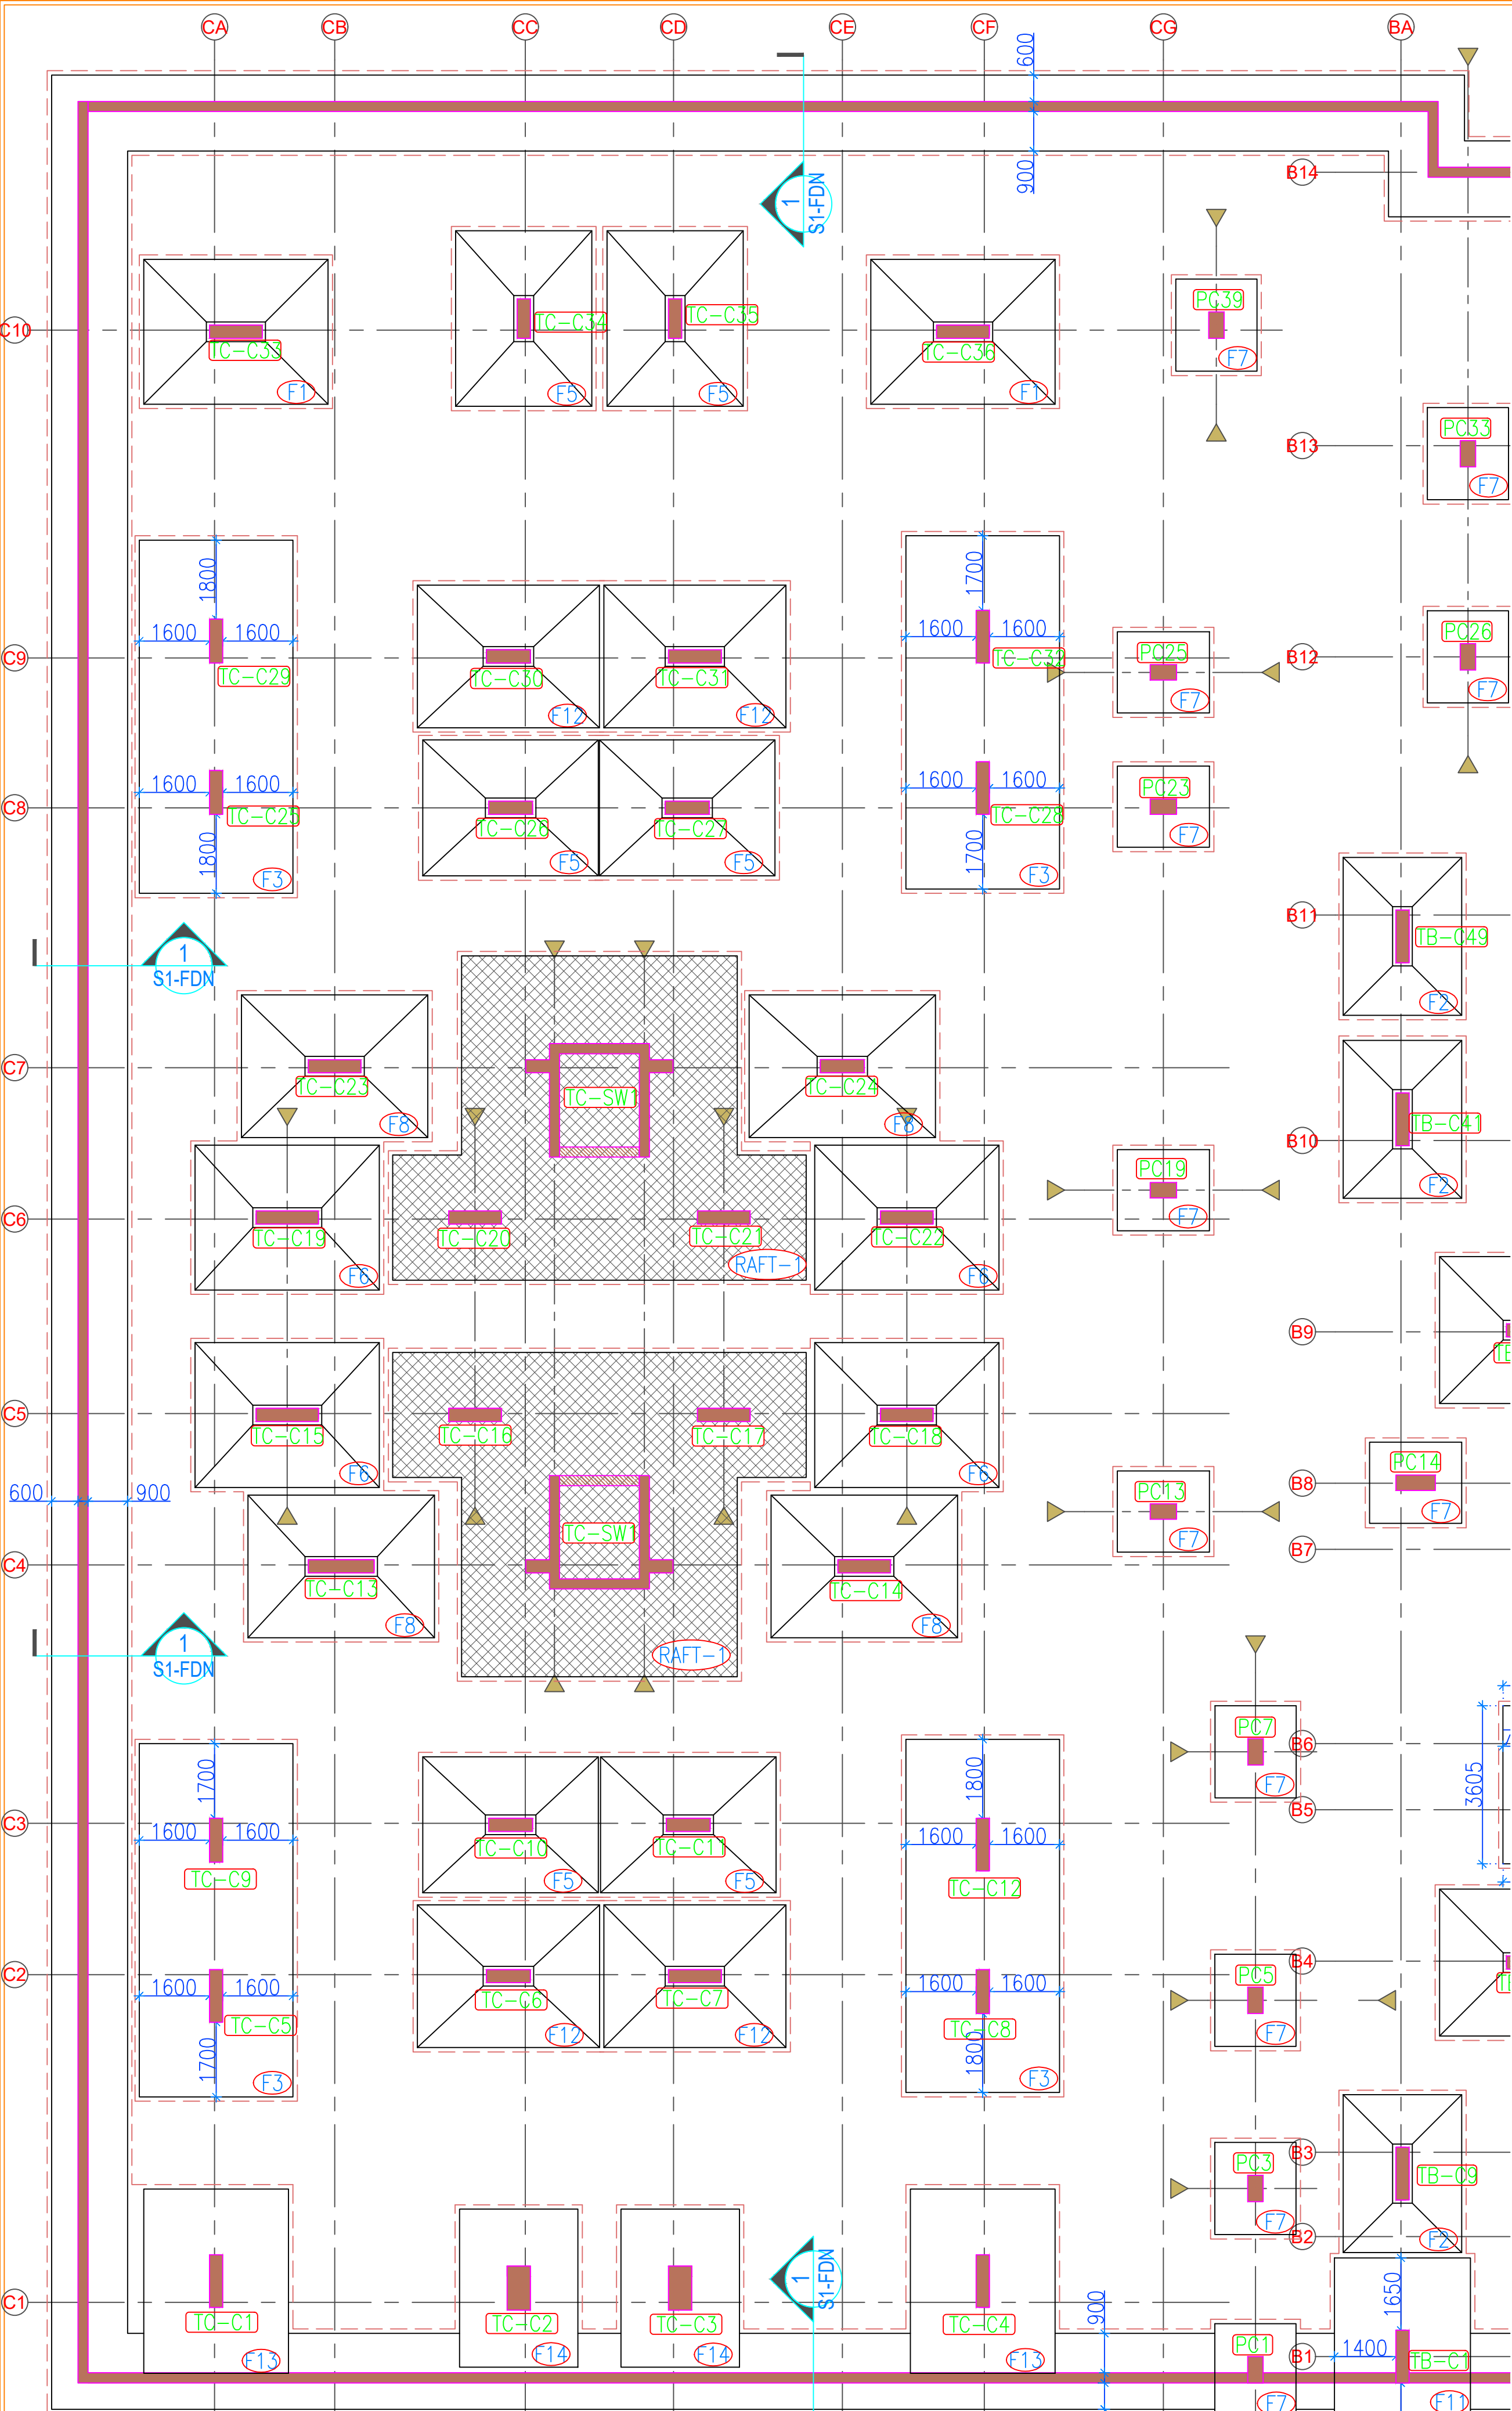

STRUCTURAL LAYOUT PLAN AT FOUNDATION LEVEL


*ALL CENTERLINE & COLUMNS / SW LOCATIONS AS PER ARCHITECTURAL DRAWINGS.

*COLUMNS / SW SIZES & R/F. SHOULD BE AS PER STRUCTURAL DRAWINGS ONLY.


COLUMN SIZES (BLOCK - C)	
COLUMN MARK	SIZES
TC-C1, TC-C4, TC-C5, TC-C6, TC-C7, TC-C14, TC-C16, TC-C17, TC-C18, TC-C20, TC-C21, TC-C22, TC-C23, TC-C28, TC-C31, TC-C32, TC-C33, TC-C36	300 X 1200
TC-C8, TC-C9, TC-C10, TC-C11, TC-C12, TC-C24, TC-C25, TC-C26, TC-C27, TC-C29, TC-C30	300 X 1000
TC-C2, TC-C3	530 X 1000
TC-C13	300 X 1500
TC-C15, TC-C19	300 X 1420
TC-C34, TC-C35	300 X 900
TC-SW1	AS PER SHAPE

COLUMN SIZES (NON-TOWER)	
COLUMN MARK	SIZES
PC1 TO PC8, PC11 TO PC13, PC17 TO PC45	350 X 600
PC9, PC10, PC15	300 X 600
PC14	350 X 900
PC16	300 X 935

LEGEND	
	COLUMN/WALL
	WALL STOPS AS PER PROFILE
	FOOTING AT DEFERENT LEVEL
	FOOTING LINE
	P.C.C LINE

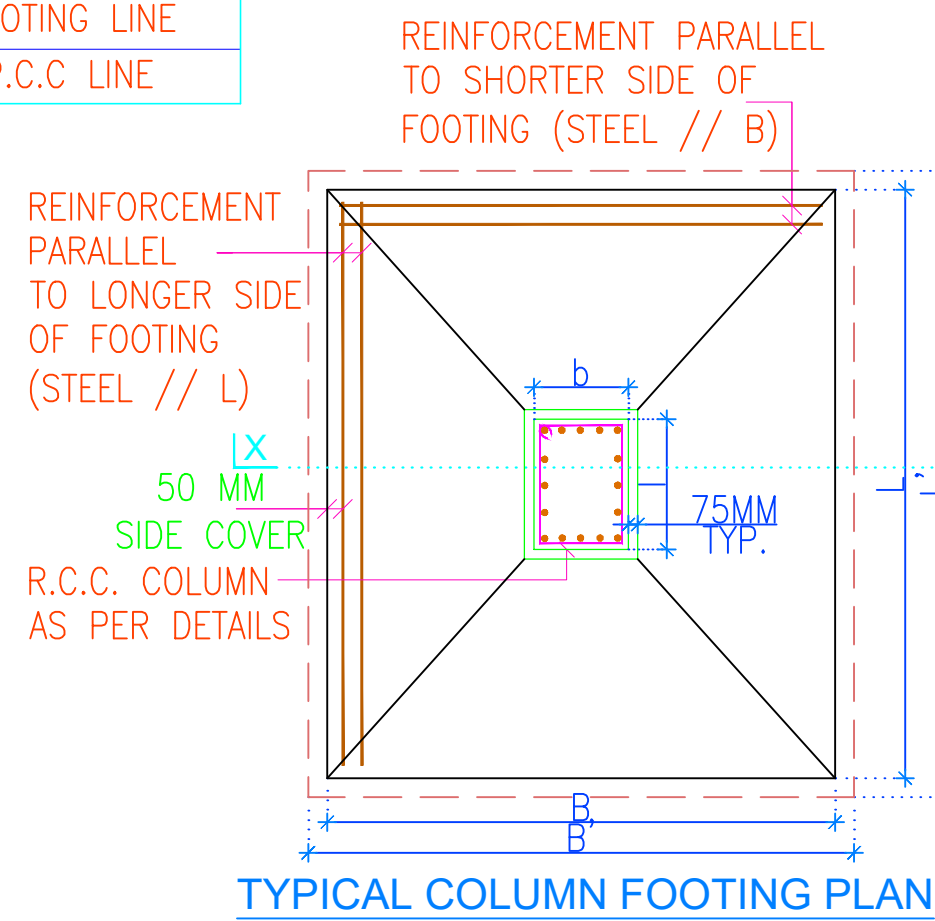


db = DIA METER OF THE BAR
ldc = DEVELOPMENT LENGTH
hc = HEIGHT OF COLUMN

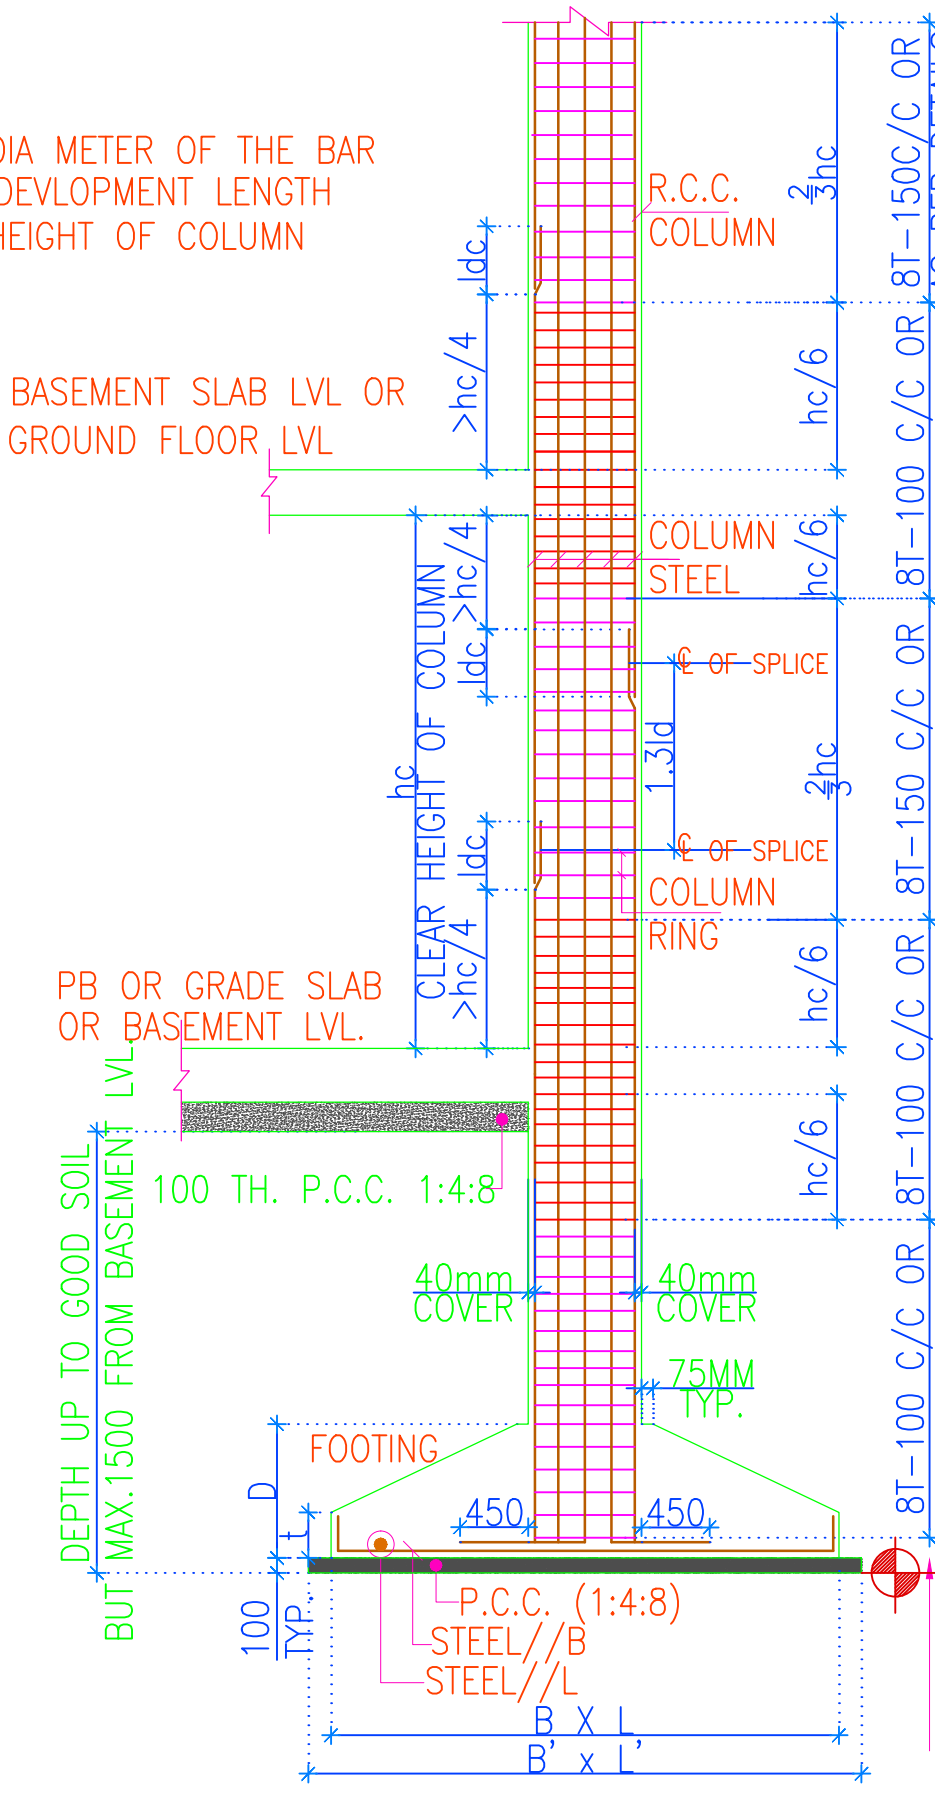


TYPICAL COLUMN FOOTING SECTION: X-X
(DUCTILITY DETAIL FOR COLUMN)
(LAPPING OF VERTICAL BARS)

- GENERAL NOTES :**
- ALL DIMENSIONS ARE IN MM.
 - ALL DIMENSIONS SHALL BE READ & NOT TO BE MEASURED.
 - ALL CONCRETING WORK SHALL BE CARRIED OUT WITH READY MIX OPC CONCRETE ONLY.
 - FOR FILLING OF SUNK OR FOR LANDSCAPING ON STRUCTURAL ELEMENTS MUST BE BY LIGHT WEIGHT CINDER FILLING ONLY HAVING THE DENSITY LESS THAN 6kN/M³.**
 - REMOVAL OF FRAMEWORK SHALL BE ONLY AFTER, ONCE CONCRETE GET MATURED ENOUGH.

- SBC NOTES :**
- NET SOIL BEARING CAPACITY IS CONSIDERED AS 350 kN/m² FROM SOIL REPORT SUBMITTED BY KBM ENGINEERING CONSULTANCY SERVICES.**
 - GROSS SBC IS CONSIDERED AS 440 kN/m² FOR FOUNDATION DESIGN.**
 - PARTIAL PERCENTAGE OF BEARING CAPACITY INCREMENT SHALL BE CONSIDERED FOR EARTHQUAKE FORCES.
 - DE-WATERING SHALL BE APPLICABLE IN CASE OF WATER TABLE FOUND AT FOUNDATION LEVEL BEFORE PACING OF CONCRETE.
 - SURFACE OF EXCAVATION SHALL BE LEVELED PROPERLY BEFORE PCC WORK.
 - RUBBLE SOLING IS RECOMMENDED, IF SOIL IS FOUND AS SANDY OR IF WATER TABLE IS PRESENCE.

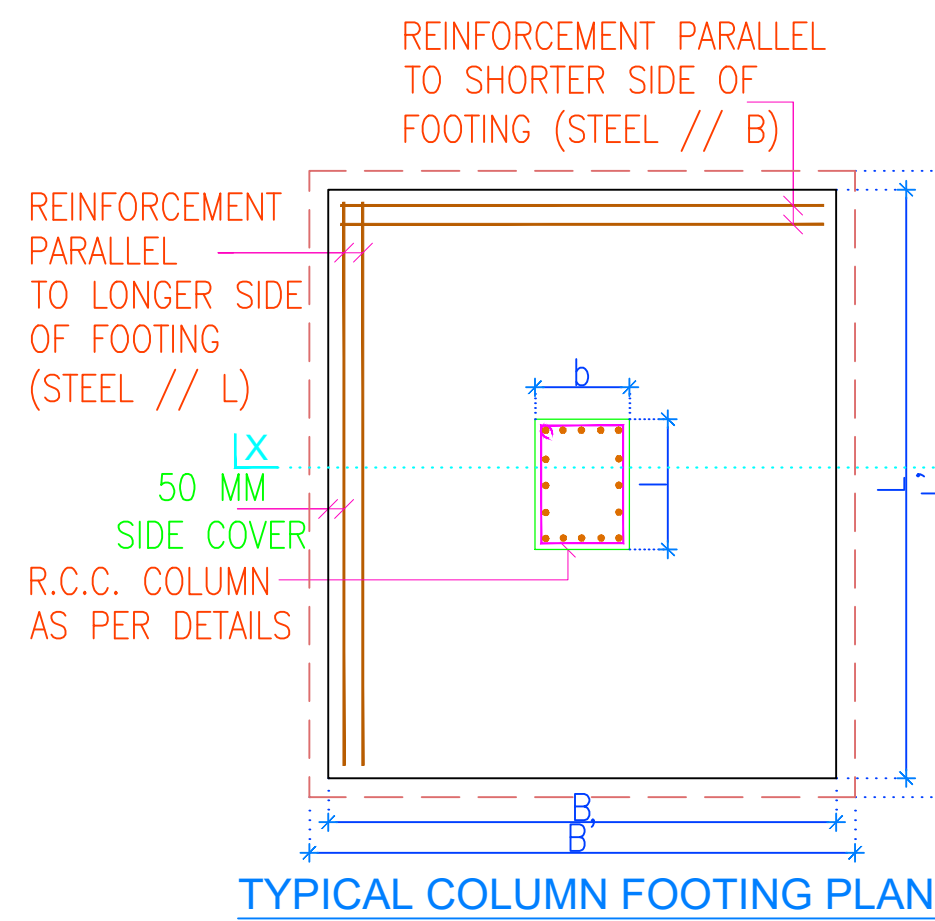


db = DIA METER OF THE BAR
ldc = DEVELOPMENT LENGTH
hc = HEIGHT OF COLUMN

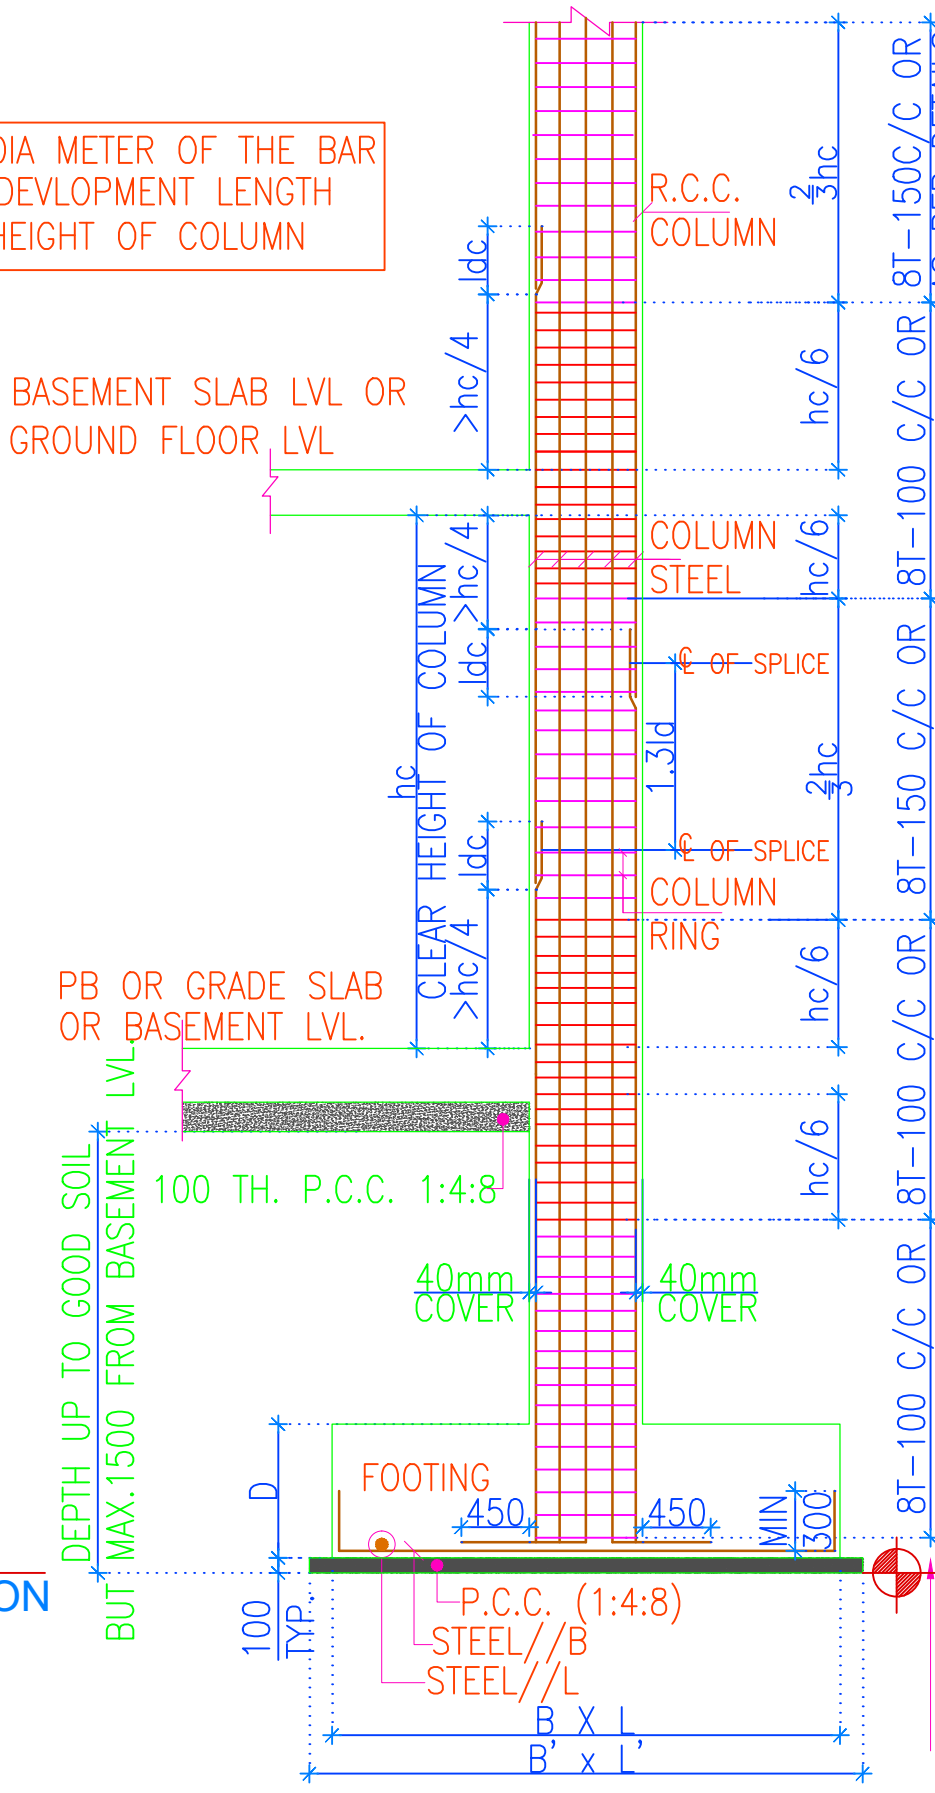

TYPICAL COLUMN FOOTING SECTION: X-X
(DUCTILITY DETAIL FOR COLUMN)
(LAPPING OF VERTICAL BARS)

- GENERAL NOTES :-**
- ALL DIMENSIONS ARE IN MM.
 - FOR ALL NOTES, REFER OUR DRG NO: S0-01 TO S0-09.
 - CEMENT SHALL BE OPC 43 GRADE OR HIGHER / AS PER TENDER SPECIFICATIONS & PORTABLE WATER SHOULD BE USE.
 - SUPERVISION SHALL NOT BE OUR RESPONSIBILITY.
 - TO TAKE OUT THE CUBE AND MATERIAL TESTING SHALL BE CONTRACTOR/ BUILDER/CLIENTS RESPONSIBILITY.
 - LOAD TESTING OF STRUCTURE SHALL NOT BE OUR RESPONSIBILITY.
 - ALL DIMENSIONS ARE TO BE READ AND NOT TO BE MEASURED
 - T OR # INDICATE STEEL FE 500D GRADE TMT BARS.
 - ALL CONC.MIX. M:30 UNLESS OTHERWISE SPECIFIED.
 - LD = DEVELOPMENT LENGTH : 50 X ϕ , WHERE, ϕ = DIA. OF BAR.
 - ALL BRICK WORK SHALL BE IN C.M. (1:6)
 - STRUCTURAL LAY OUT SHOULD BE REFER ONLY FOR STRUCTURAL DETAILING.
 - PLEASE REFER ARCHITECTURAL DWG FOR LVLS. & SETTINGS OUT CENTERLINE DIMENSIONS. THE CENTERLINE PUT IN THIS STRUCTURAL FOUNDATION LAYOUT IS SIMPLY INDICATIVE OF LOCATION AND AS APPROVED BY ARCHITECT.
 - PLEASE REFER ARCH. DWG. FOR FINAL LAY OUT.
 - CONTRACTOR SHOULD INFORM ARCHITECT/STRUCTURAL CONSULTANT IN CASE OF ANY CHANGE IN EXISTING CONDITION FOUND, IMMEDIATELY
 - THIS DRG. SHOULD BE READ ALONG WITH ARCHITECTURAL DRGS. AND ANY CHANGES/DEVIATION FOUND SHOULD BE IMMEDIATELY BROUGHT TO NOTICE OF ARCHITECT & STR. ENGINEER
 - THIS DRG. SHOULD BE READ ALONG WITH RELEVANT DETAILS
 - MIX DESIGN SHOULD BE GOT APPROVED PRIOR TO EXECUTION OF WORK
 - ALL STEEL (TOP/BOTTOM) OF DIFFERENT ZONE SHALL BE LAPPED IN ADDITION WHERE THE ZONE TERMINATES; BY LENGTH EQUAL TO THE DEVELOPMENT LENGTH OF HIGHER DIA BAR.

KEY PLAN

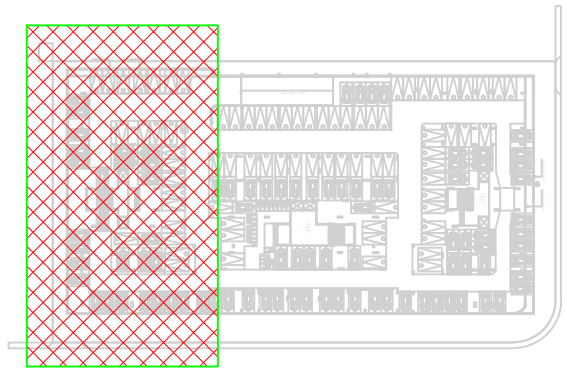


GRADE OF CONCRETE

ALL STRUCTURAL ELEMENTS	M30
-------------------------	-----

CONCRETE COVER

FOOTINGS /RAFT	50MM
COLUMNS/SW	40MM
BEAMS	30MM
SLABS	25MM
PARDI WALLS	30MM

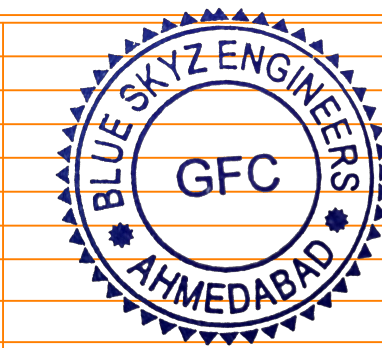

2	10-12-21	GOOD FOR CONSTRUCTION
1	08-12-21	FOR REVIEW ONLY
NO.	DATE	REVISION / REMARK
		BY DR CH

JOB TITLE / DEVELOPER

TURQUOISE-GRANDEUR
RATANA DEVELOPERS

DRAWING TITLE

STRUCTURAL LAYOUT AT FOUNDATION LEVEL

JOB NO	DATE	DRG. NO.	REVISION
2111	16/04/2021	S1-FDN-01	R0
SCALE	SHEET SIZE	DRAWN	DESIGN
1:100	A1/A2/A3	BP	KUNJ
ARCHITECTS	CHECKED		BHAVIK PATEL



HM ARCHITECTS
e:contact@hmarchitects.in

STRUCTURAL CONSULTANT



email:blueskyzengineers@gmail.com