
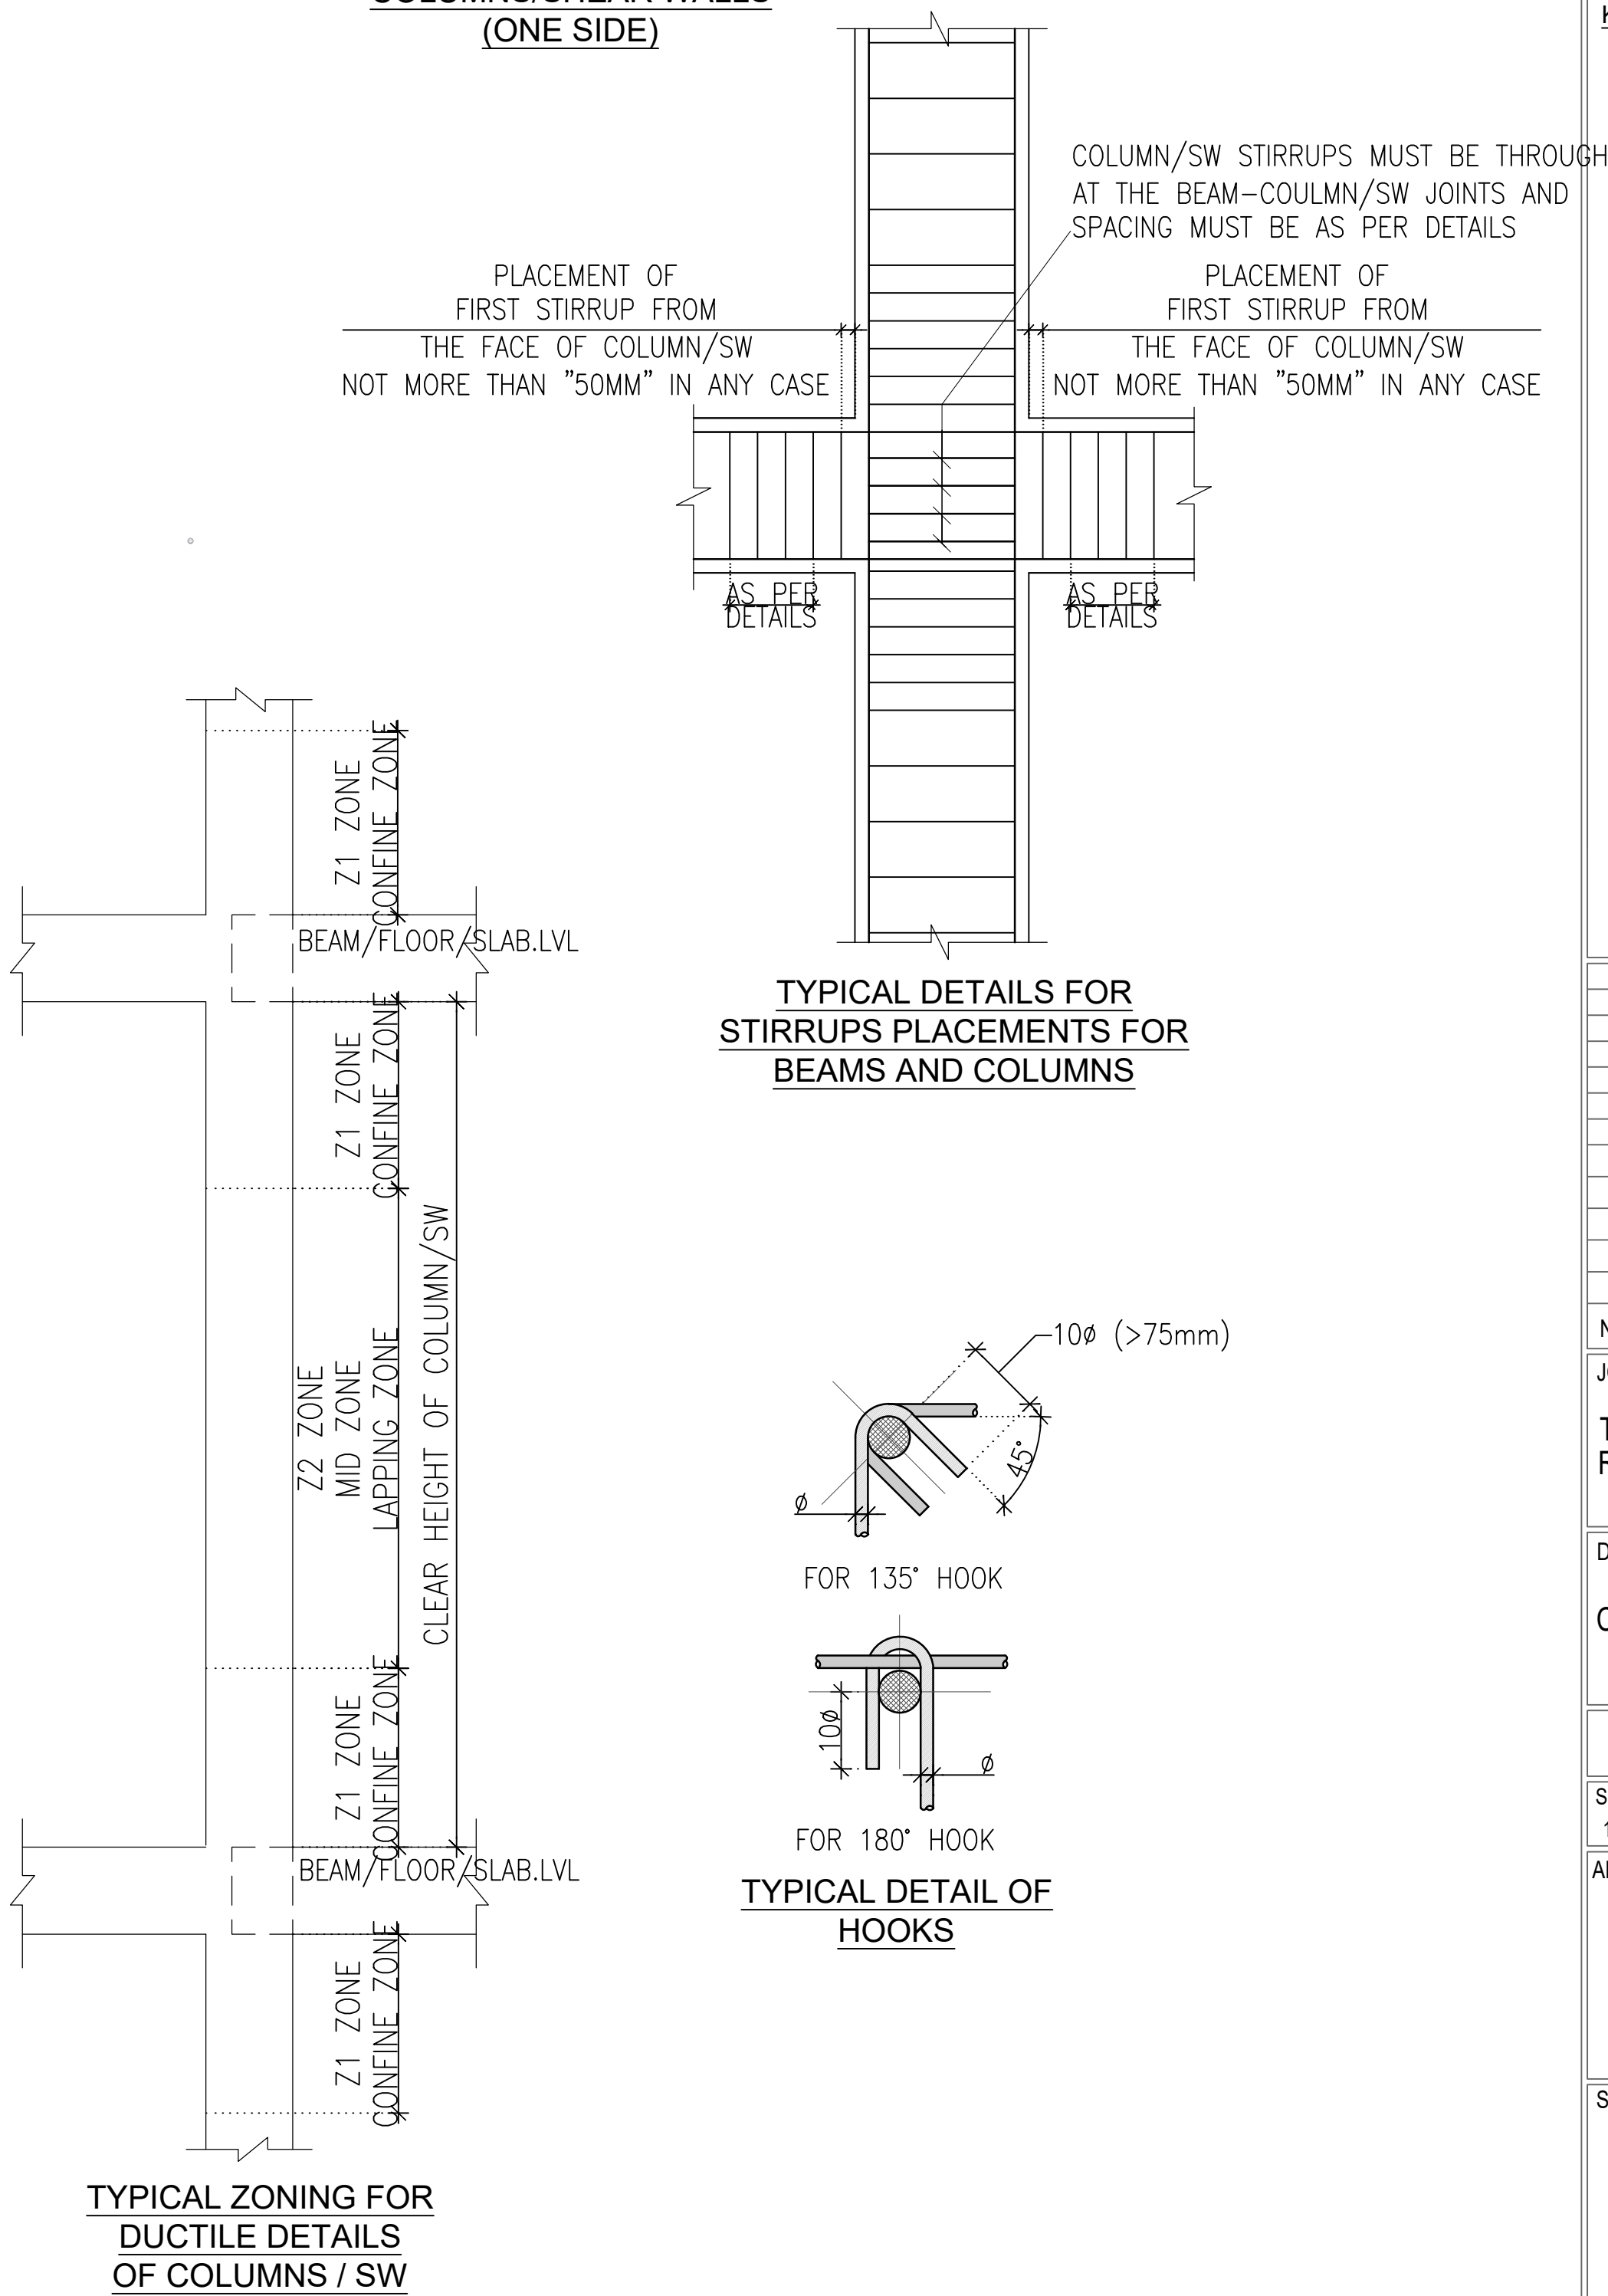


<u>GRADE OF CONCRETE FOR</u> COLUMNS/SW - M35 UP TO 4TH FLOOR	
---	--


COLUMN FROM THIRD FLOOR LVL. TO FOURTH FLOOR LVL.	CONCRETE MIX – M30		● 8-25T ⊗ 16-20T					
		COL. RING/LINK	● 4-25T ⊗ 16-20T					
		8T-100 C/C (8 NOS.-Z1) 8T-100 C/C (AT MID-Z2)						
COLUMN FROM SECOND FLOOR LVL. TO THIRD FLOOR LVL.	CONCRETE MIX – M30		● 8-25T ⊗ 16-20T					
		COL. RING/LINK	● 4-25T ⊗ 16-20T					
		8T-100 C/C (8 NOS.-Z1) 8T-100 C/C (AT MID-Z2)						
COLUMN FROM FIRST FLOOR LVL. TO SECOND FLOOR LVL.	CONCRETE MIX – M30		● 20-20T ⊗ 4-16T					
		COL. RING/LINK	● 20-20T ⊗ 4-16T					
		8T-100 C/C (8 NOS.-Z1) 8T-100 C/C (AT MID-Z2)						
COLUMN FROM GROUND FLOOR LVL. TO FIRST FLOOR LVL.	CONCRETE MIX – M30		● 4-25T ⊗ 16-20T					
		COL. RING/LINK	● 4-25T ⊗ 16-20T					
		8T-100 C/C (8 NOS.-Z1) 8T-100 C/C (AT MID-Z2)						
COLUMN FROM FOUNDATION LVL. TO GROUND FLOOR LVL.	CONCRETE MIX – M30		● 8-16T ⊗ 22-12T					
		COL. RING/LINK	● 8-16T ⊗ 22-12T					
		8T-100 C/C (8 NOS.-Z1) 8T-100 C/C (AT MID-Z2)						
COLUMN FROM FOUNDATION LVL. TO GROUND FLOOR LVL.	CONCRETE MIX – M30		● 16-16T ⊗ 4-12T					
		COL. RING/LINK	● 16-16T ⊗ 4-12T					
		8T-100 C/C (8 NOS.-Z1) 8T-100 C/C (AT MID-Z2)						
COLUMN FROM FOUNDATION LVL. TO GROUND FLOOR LVL.	CONCRETE MIX – M30		● 8-25T ⊗ 16-20T					
		COL. RING/LINK	● 8-25T ⊗ 16-20T					
		8T-100 C/C (8 NOS.-Z1) 8T-100 C/C (AT MID-Z2)						
COLUMN		TA-C6, TA-C30	TA-C7, TA-C31	TA-C8, TA-C32	TA-C10, TA-C11, TA-C26, TA-C27	TA-C13	TA-C14, TA-C24	TA-C9, TA-C25

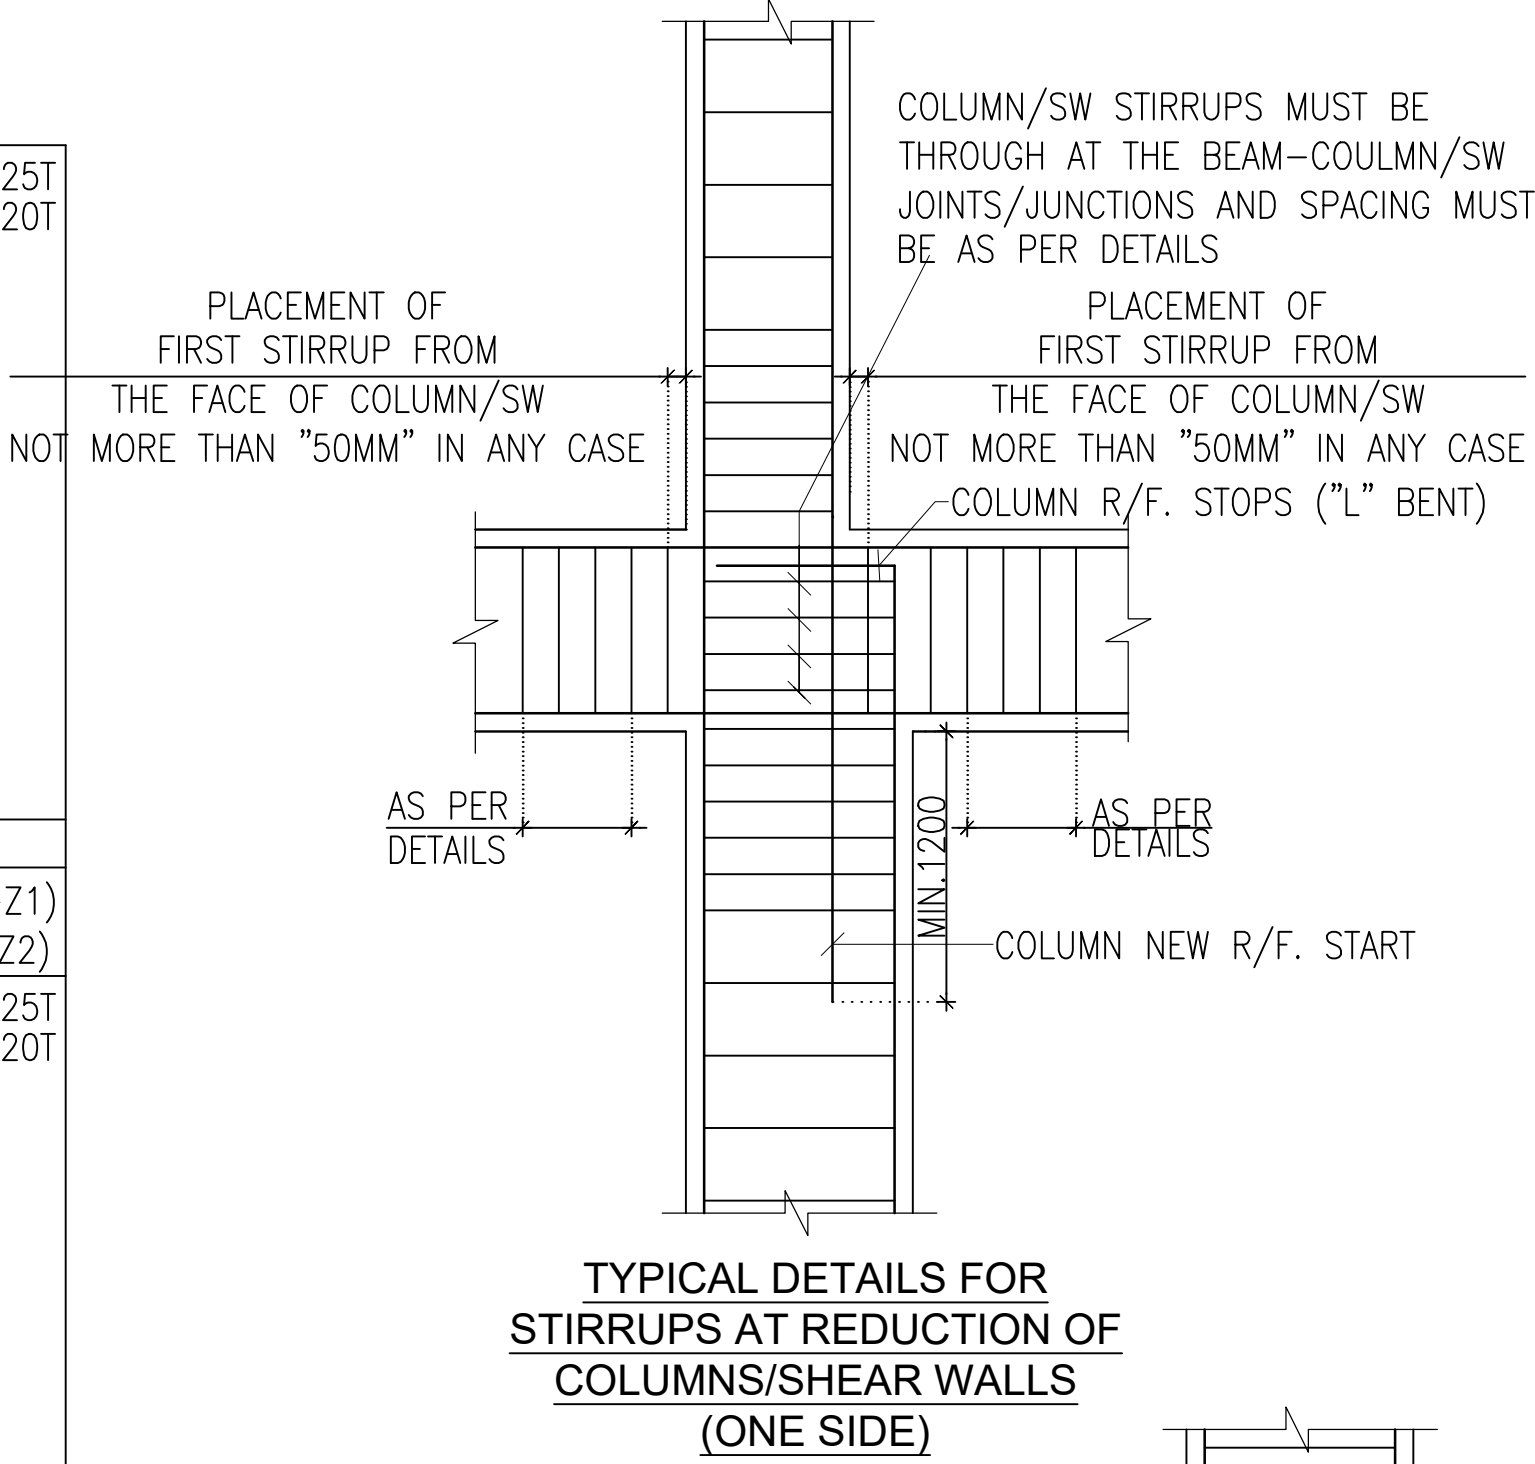

GENERAL NOTES :-


1. ALL DIMENSIONS ARE IN MM.
2. FOR ALL NOTES, REFER OUR DRG NO: S0-01 TO S0-09.
3. CEMENT SHALL BE OPC 43 GRADE OR HIGHER / AS PER TENDER SPECIFICATIONS & PORTABLE WATER SHOULD BE USE.
4. SUPERVISION SHALL NOT BE OUR RESPONSIBILITY.
5. TO TAKE OUT THE CUBE AND MATERIAL TESTING SHALL BE CONTRACTOR/ BUILDER/CLIENTS RESPONSIBILITY.
6. LOAD TESTING OF STRUCTURE SHALL NOT BE OUR RESPONSIBILITY.
7. ALL DIMENSIONS ARE TO BE READ AND NOT TO BE MEASURED
8. T OR ϕ INDICATE STEEL FE 5000 GRADE TMT BARS.
9. ALL CONC.MIX. M:30 UNLESS OTHERWISE SPECIFIED.
- 10.LD = DEVELOPMENT LENGTH : $50 \times \phi$; WHERE, ϕ = DIA. OF BAR.
- 11.ALL BRICK WORK SHALL BE IN C.M. (1:6)
- 12.STRUCTURAL LAY OUT SHOULD BE REFER ONLY FOR STRUCTURAL DETAILING.
- 13.PLEASE REFER ARCHITECTURAL DWG FOR LVLS. & SETTINGS OUT CENTERLINE DIMENSIONS. THE CENTERLINE PUT IN THIS STRUCTURAL FOUNDATION LAYOUT IS SIMPLY INDICATIVE OF LOCATION AND AS APPROVED BY ARCHITECT.
- 14.PLEASE REFER ARCH. DWG. FOR FINAL LAY OUT.
- 15.CONTRACTOR SHOULD INFORM ARCHITECT/STRUCTURAL CONSULTANT IN CASE OF ANY CHANGE IN EXISTING CONDITION FLOW, IMMEDIATELY.
- 16.THIS DRG. SHOULD BE READ ALONG WITH ARCHITECTURAL DRGS AND ANY CHANGES/DEVIATION FOUND SHOULD BE IMMEDIATELY BROUGHT TO NOTICE OF ARCHITECT & STR. ENGINEER
- 17.THIS DRG.SHOULD BE READ ALONG WITH RELEVANT DETAILS
- 18.MIX DESIGN SHOULD BE GOT APPROVED PRIOR TO EXECUTION OF WORK
- 19.ALL STEEL (TOP/BOTTOM) OF DIFFERENT ZONE SHALL BE LAPPED IN ADDITION WHERE THE ZONE TERMINATES; BY LENGTH EQUAL TO THE DEVELOPMENT LENGTH OF HIGHER DIA. BAR.

KEY PLAN

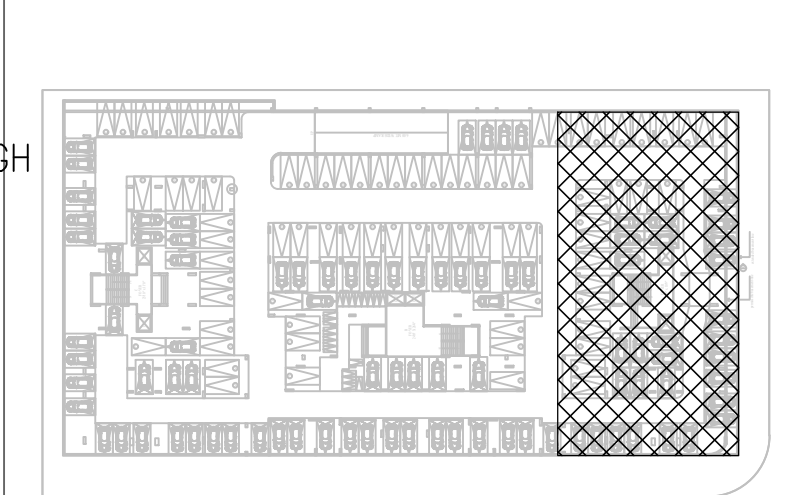

GRADE OF CONCRETE	
ALL STRUCTURAL ELEMENTS	M35

CONCRETE COVER	
FOOTINGS /RAFT	50MM
COLUMNS/SW	40MM
BEAMS	30MM
SLABS	25MM
PARDI WALLS	30MM

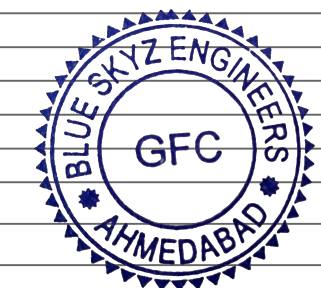

1	29-12-21	GOOD FOR CONSTRUCTION			
NO.	DATE	REVISION / REMARK	BY	DR	CH

JOB TITLE / DEVELOPER

TURQUOISE-GRANDEUR
RATANA DEVELOPERS

DRAWING TITLE

COLUMN SCHEDULE DETAIL - TOWER-A


JOB NO 2111		DATE 16/04/2021		DRG. NO. S5-TA-04		REVISION R0	
SCALE 1 : 100	SHEET SIZE A1/A2/A3	DRAWN AKSHAY		DESIGN KUNJ		CHECKED BHAVIK PATEL	

ARCHITECTS



HM ARCHITECTS
e:contact@hmmarchitects.in

STRUCTURAL CONSULTANT

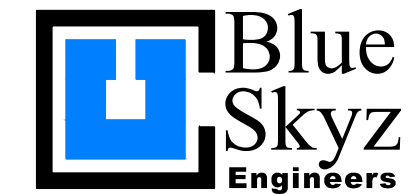

email:blueskyzengineers@gmail.com