

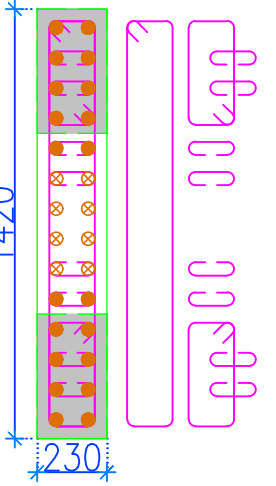
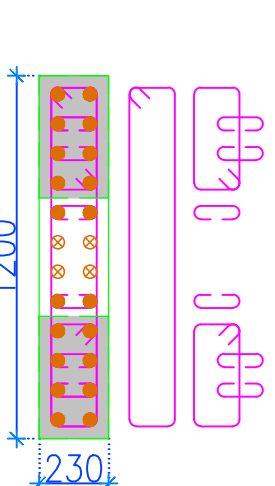
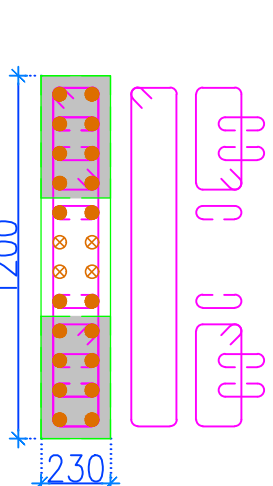
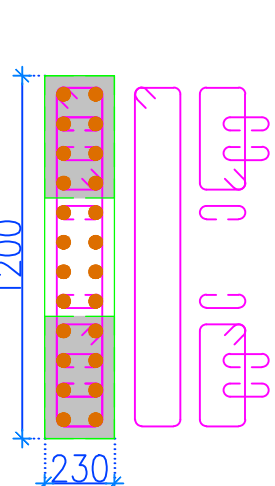
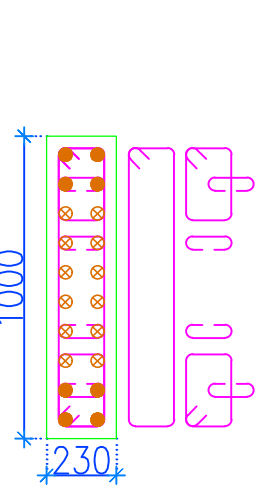
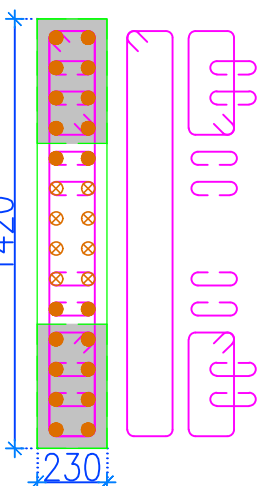
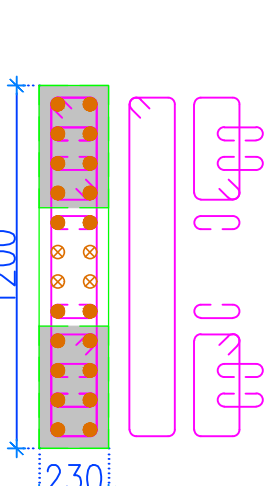
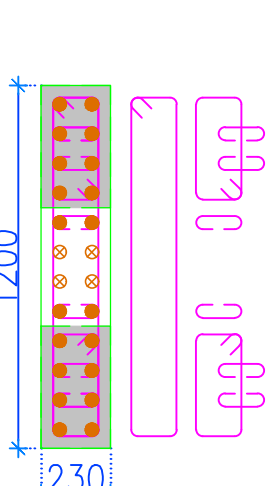
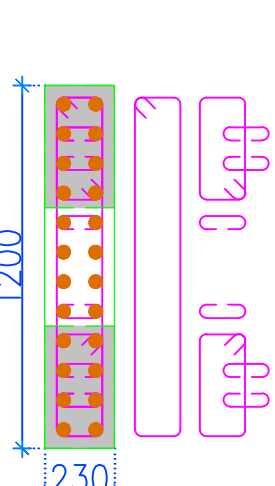
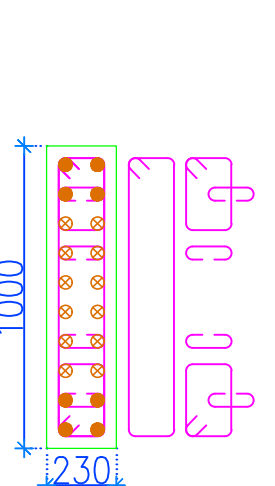
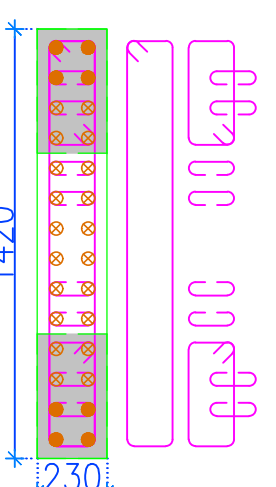
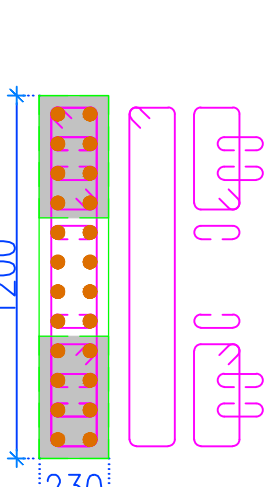
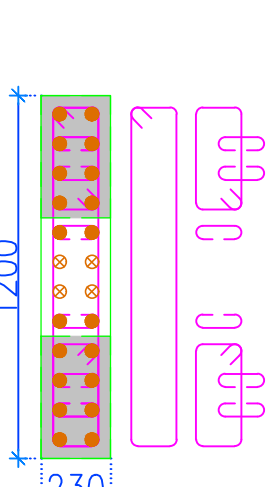
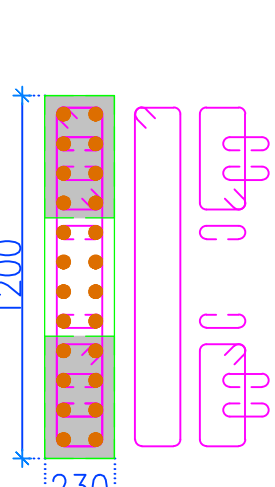
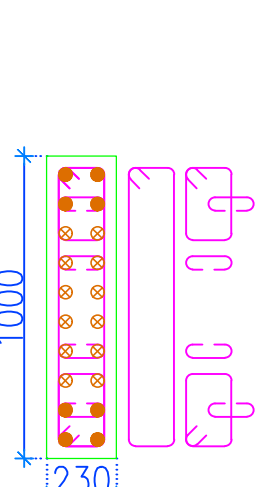
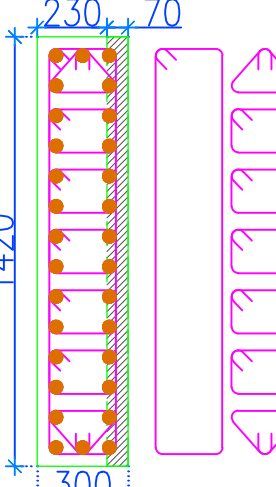
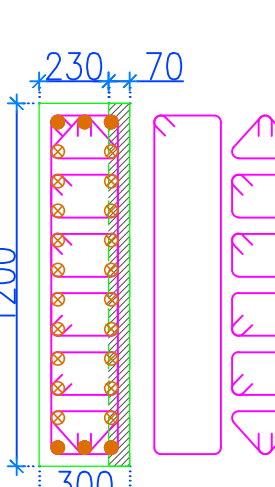
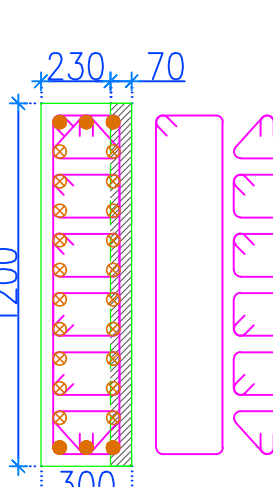
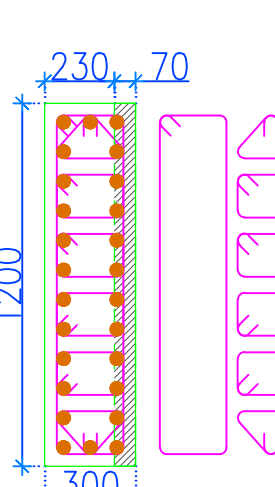
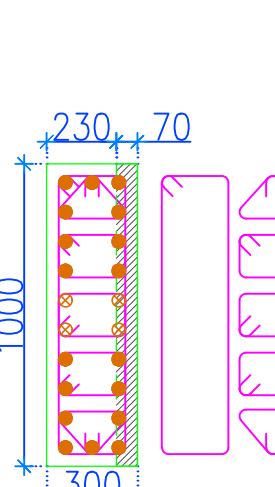
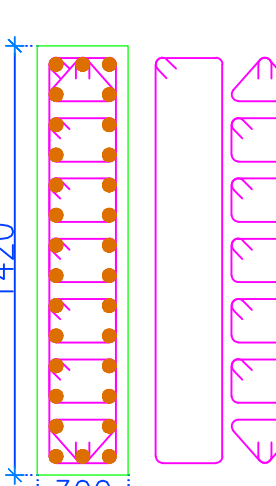
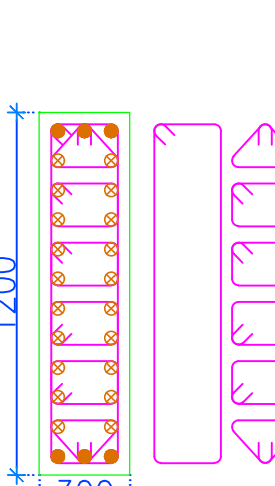
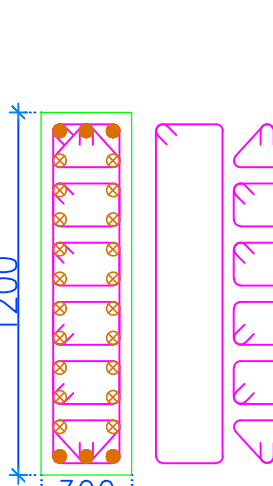
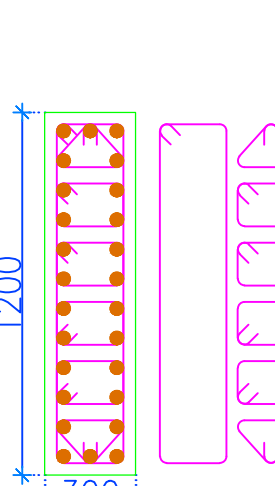
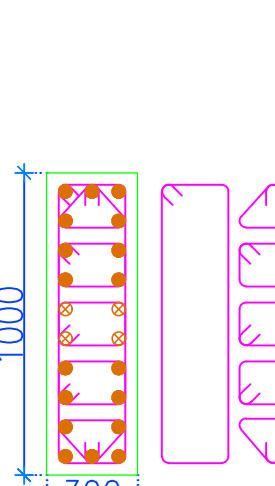


GRADE OF CONCRETE FOR
COLUMNS/SW - M35 UP TO 4TH FLOOR


COLUMN FROM THIRD FLOOR LVL. TO FOURTH FLOOR LVL.	CONCRETE MIX – M30	● 20–16T ⊗ 8–12T 	● 20–20T ⊗ 4–16T 	● 20–16T ⊗ 4–12T 	● 24–12T 	● 8–20T ⊗ 12–16T 	COL. RING/LINK 8T–100 C/C (8 NOS.–Z1) 8T–100 C/C (AT MID–Z2)	COL. RING/LINK 8T–100 C/C (8 NOS.–Z1) 8T–100 C/C (AT MID–Z2)	COL. RING/LINK 8T–100 C/C (8 NOS.–Z1) 8T–100 C/C (AT MID–Z2)	COL. RING/LINK 8T–100 C/C (8 NOS.–Z1) 8T–100 C/C (AT MID–Z2)	COL. RING/LINK 8T–100 C/C (8 NOS.–Z1) 8T–100 C/C (AT MID–Z2)
		● 20–16T ⊗ 8–12T 	● 20–20T ⊗ 4–16T 	● 20–16T ⊗ 4–12T 	● 24–12T 	● 8–20T ⊗ 12–16T 	COL. RING/LINK 8T–100 C/C (8 NOS.–Z1) 8T–100 C/C (AT MID–Z2)	COL. RING/LINK 8T–100 C/C (8 NOS.–Z1) 8T–100 C/C (AT MID–Z2)	COL. RING/LINK 8T–100 C/C (8 NOS.–Z1) 8T–100 C/C (AT MID–Z2)	COL. RING/LINK 8T–100 C/C (8 NOS.–Z1) 8T–100 C/C (AT MID–Z2)	COL. RING/LINK 8T–100 C/C (8 NOS.–Z1) 8T–100 C/C (AT MID–Z2)
COLUMN FROM SECOND FLOOR LVL. TO THIRD FLOOR LVL.	CONCRETE MIX – M30	● 20–16T ⊗ 8–12T 	● 20–20T ⊗ 4–16T 	● 20–16T ⊗ 4–12T 	● 24–12T 	● 8–20T ⊗ 12–16T 	COL. RING/LINK 8T–100 C/C (8 NOS.–Z1) 8T–100 C/C (AT MID–Z2)	COL. RING/LINK 8T–100 C/C (8 NOS.–Z1) 8T–100 C/C (AT MID–Z2)	COL. RING/LINK 8T–100 C/C (8 NOS.–Z1) 8T–100 C/C (AT MID–Z2)	COL. RING/LINK 8T–100 C/C (8 NOS.–Z1) 8T–100 C/C (AT MID–Z2)	COL. RING/LINK 8T–100 C/C (8 NOS.–Z1) 8T–100 C/C (AT MID–Z2)
		● 8–20T ⊗ 20–16T 	● 24–20T 	● 20–16T ⊗ 4–12T 	● 24–12T 	● 8–20T ⊗ 12–16T 	COL. RING/LINK 8T–100 C/C (8 NOS.–Z1) 8T–100 C/C (AT MID–Z2)	COL. RING/LINK 8T–100 C/C (8 NOS.–Z1) 8T–100 C/C (AT MID–Z2)	COL. RING/LINK 8T–100 C/C (8 NOS.–Z1) 8T–100 C/C (AT MID–Z2)	COL. RING/LINK 8T–100 C/C (8 NOS.–Z1) 8T–100 C/C (AT MID–Z2)	COL. RING/LINK 8T–100 C/C (8 NOS.–Z1) 8T–100 C/C (AT MID–Z2)
COLUMN FROM FIRST FLOOR LVL. TO SECOND FLOOR LVL.	CONCRETE MIX – M30	● 8–20T ⊗ 20–16T 	● 24–20T 	● 20–16T ⊗ 4–12T 	● 24–12T 	● 8–20T ⊗ 12–16T 	COL. RING/LINK 8T–100 C/C (8 NOS.–Z1) 8T–100 C/C (AT MID–Z2)	COL. RING/LINK 8T–100 C/C (8 NOS.–Z1) 8T–100 C/C (AT MID–Z2)	COL. RING/LINK 8T–100 C/C (8 NOS.–Z1) 8T–100 C/C (AT MID–Z2)	COL. RING/LINK 8T–100 C/C (8 NOS.–Z1) 8T–100 C/C (AT MID–Z2)	COL. RING/LINK 8T–100 C/C (8 NOS.–Z1) 8T–100 C/C (AT MID–Z2)
		● 30–20T 	● 6–25T ⊗ 20–20T 	● 6–20T ⊗ 20–16T 	● 26–12T 	● 18–20T ⊗ 4–16T 	COL. RING/LINK 8T–100 C/C (8 NOS.–Z1) 8T–100 C/C (AT MID–Z2)	COL. RING/LINK 8T–100 C/C (8 NOS.–Z1) 8T–100 C/C (AT MID–Z2)	COL. RING/LINK 8T–100 C/C (8 NOS.–Z1) 8T–100 C/C (AT MID–Z2)	COL. RING/LINK 8T–100 C/C (8 NOS.–Z1) 8T–100 C/C (AT MID–Z2)	COL. RING/LINK 8T–100 C/C (8 NOS.–Z1) 8T–100 C/C (AT MID–Z2)
COLUMN FROM GROUND FLOOR LVL. TO FIRST FLOOR LVL.	CONCRETE MIX – M30	● 30–20T	● 6–25T ⊗ 20–20T	● 6–20T ⊗ 20–16T	● 26–12T	● 18–20T ⊗ 4–16T	COL. RING/LINK 8T–100 C/C (8 NOS.–Z1) 8T–100 C/C (AT MID–Z2)	COL. RING/LINK 8T–100 C/C (8 NOS.–Z1) 8T–100 C/C (AT MID–Z2)	COL. RING/LINK 8T–100 C/C (8 NOS.–Z1) 8T–100 C/C (AT MID–Z2)	COL. RING/LINK 8T–100 C/C (8 NOS.–Z1) 8T–100 C/C (AT MID–Z2)	COL. RING/LINK 8T–100 C/C (8 NOS.–Z1) 8T–100 C/C (AT MID–Z2)
		● 30–20T	● 6–25T ⊗ 20–20T	● 6–20T ⊗ 20–16T	● 26–12T	● 18–20T ⊗ 4–16T	COL. RING/LINK 8T–100 C/C (8 NOS.–Z1) 8T–100 C/C (AT MID–Z2)	COL. RING/LINK 8T–100 C/C (8 NOS.–Z1) 8T–100 C/C (AT MID–Z2)	COL. RING/LINK 8T–100 C/C (8 NOS.–Z1) 8T–100 C/C (AT MID–Z2)	COL. RING/LINK 8T–100 C/C (8 NOS.–Z1) 8T–100 C/C (AT MID–Z2)	COL. RING/LINK 8T–100 C/C (8 NOS.–Z1) 8T–100 C/C (AT MID–Z2)
COLUMN	CONCRETE MIX – M30	TA–C15, TA–C19	TA–C12, TA–C28	TA–C16, TA–C20	TA–C18, TA–C22	TA–C17, TA–C21					

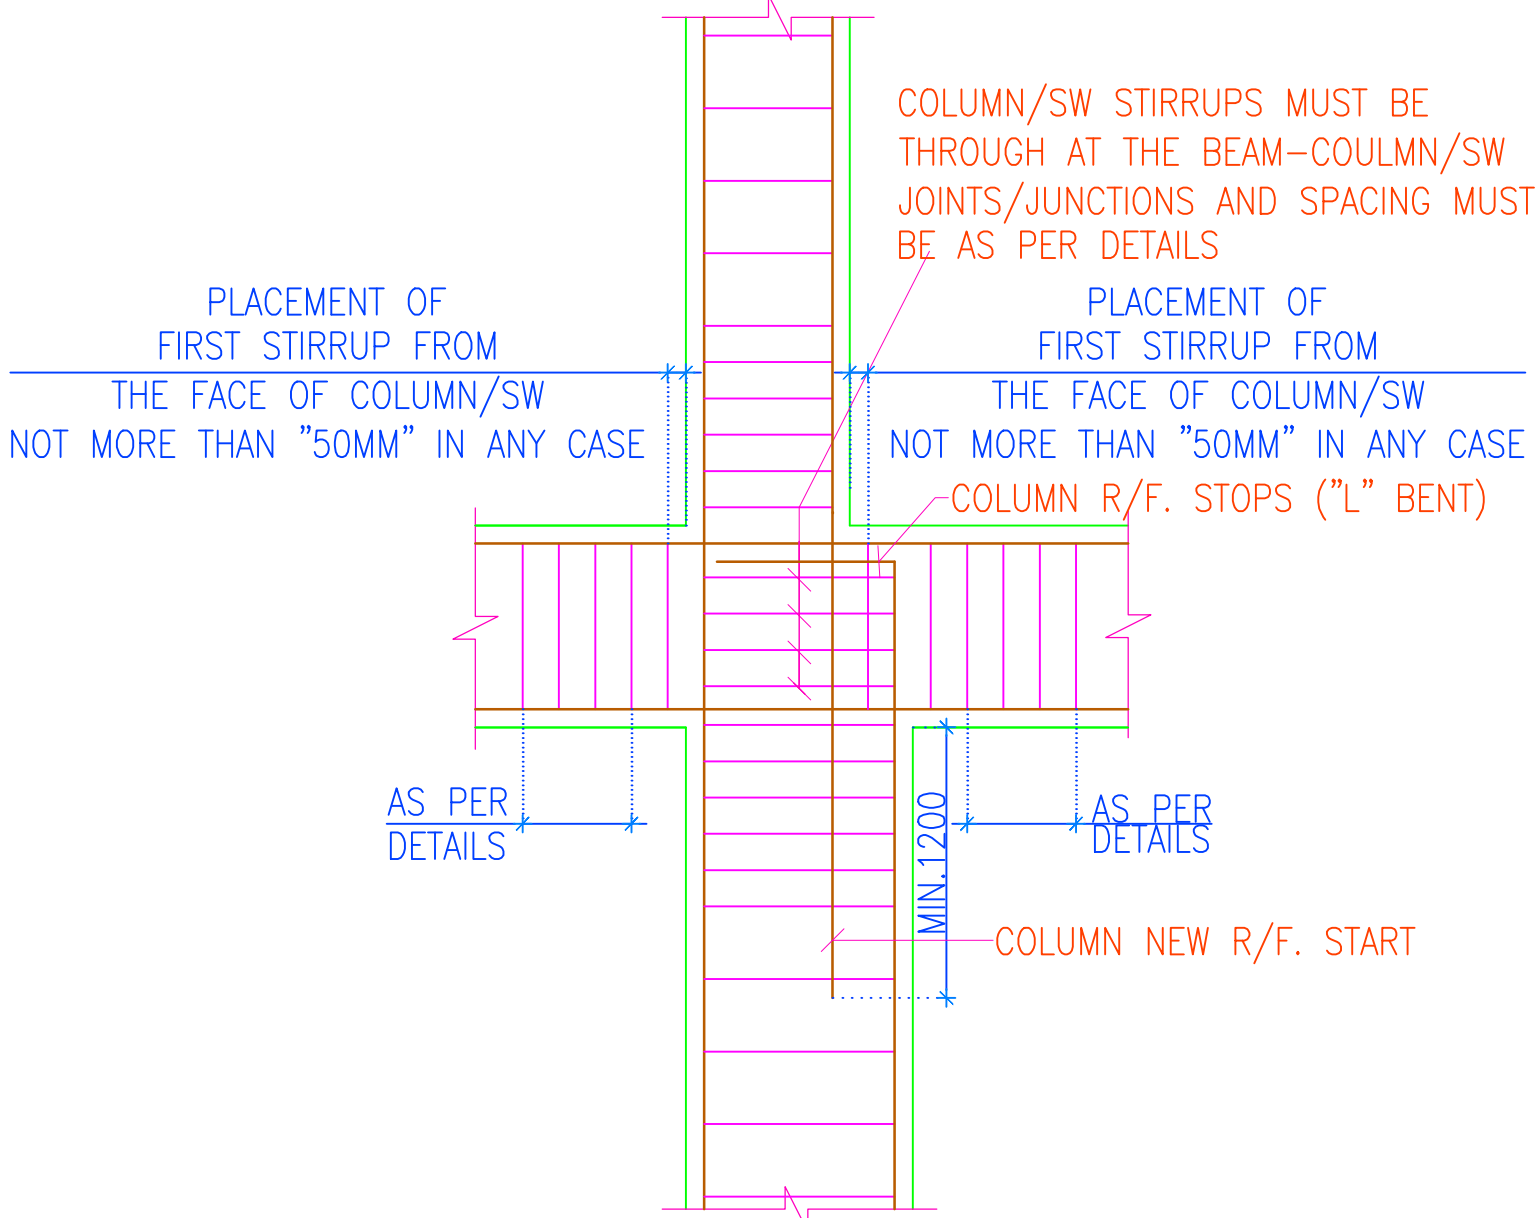


TYPICAL DETAILS FOR
STIRRUPS AT REDUCTION OF
COLUMNS/SHEAR WALLS
(ONE SIDE)

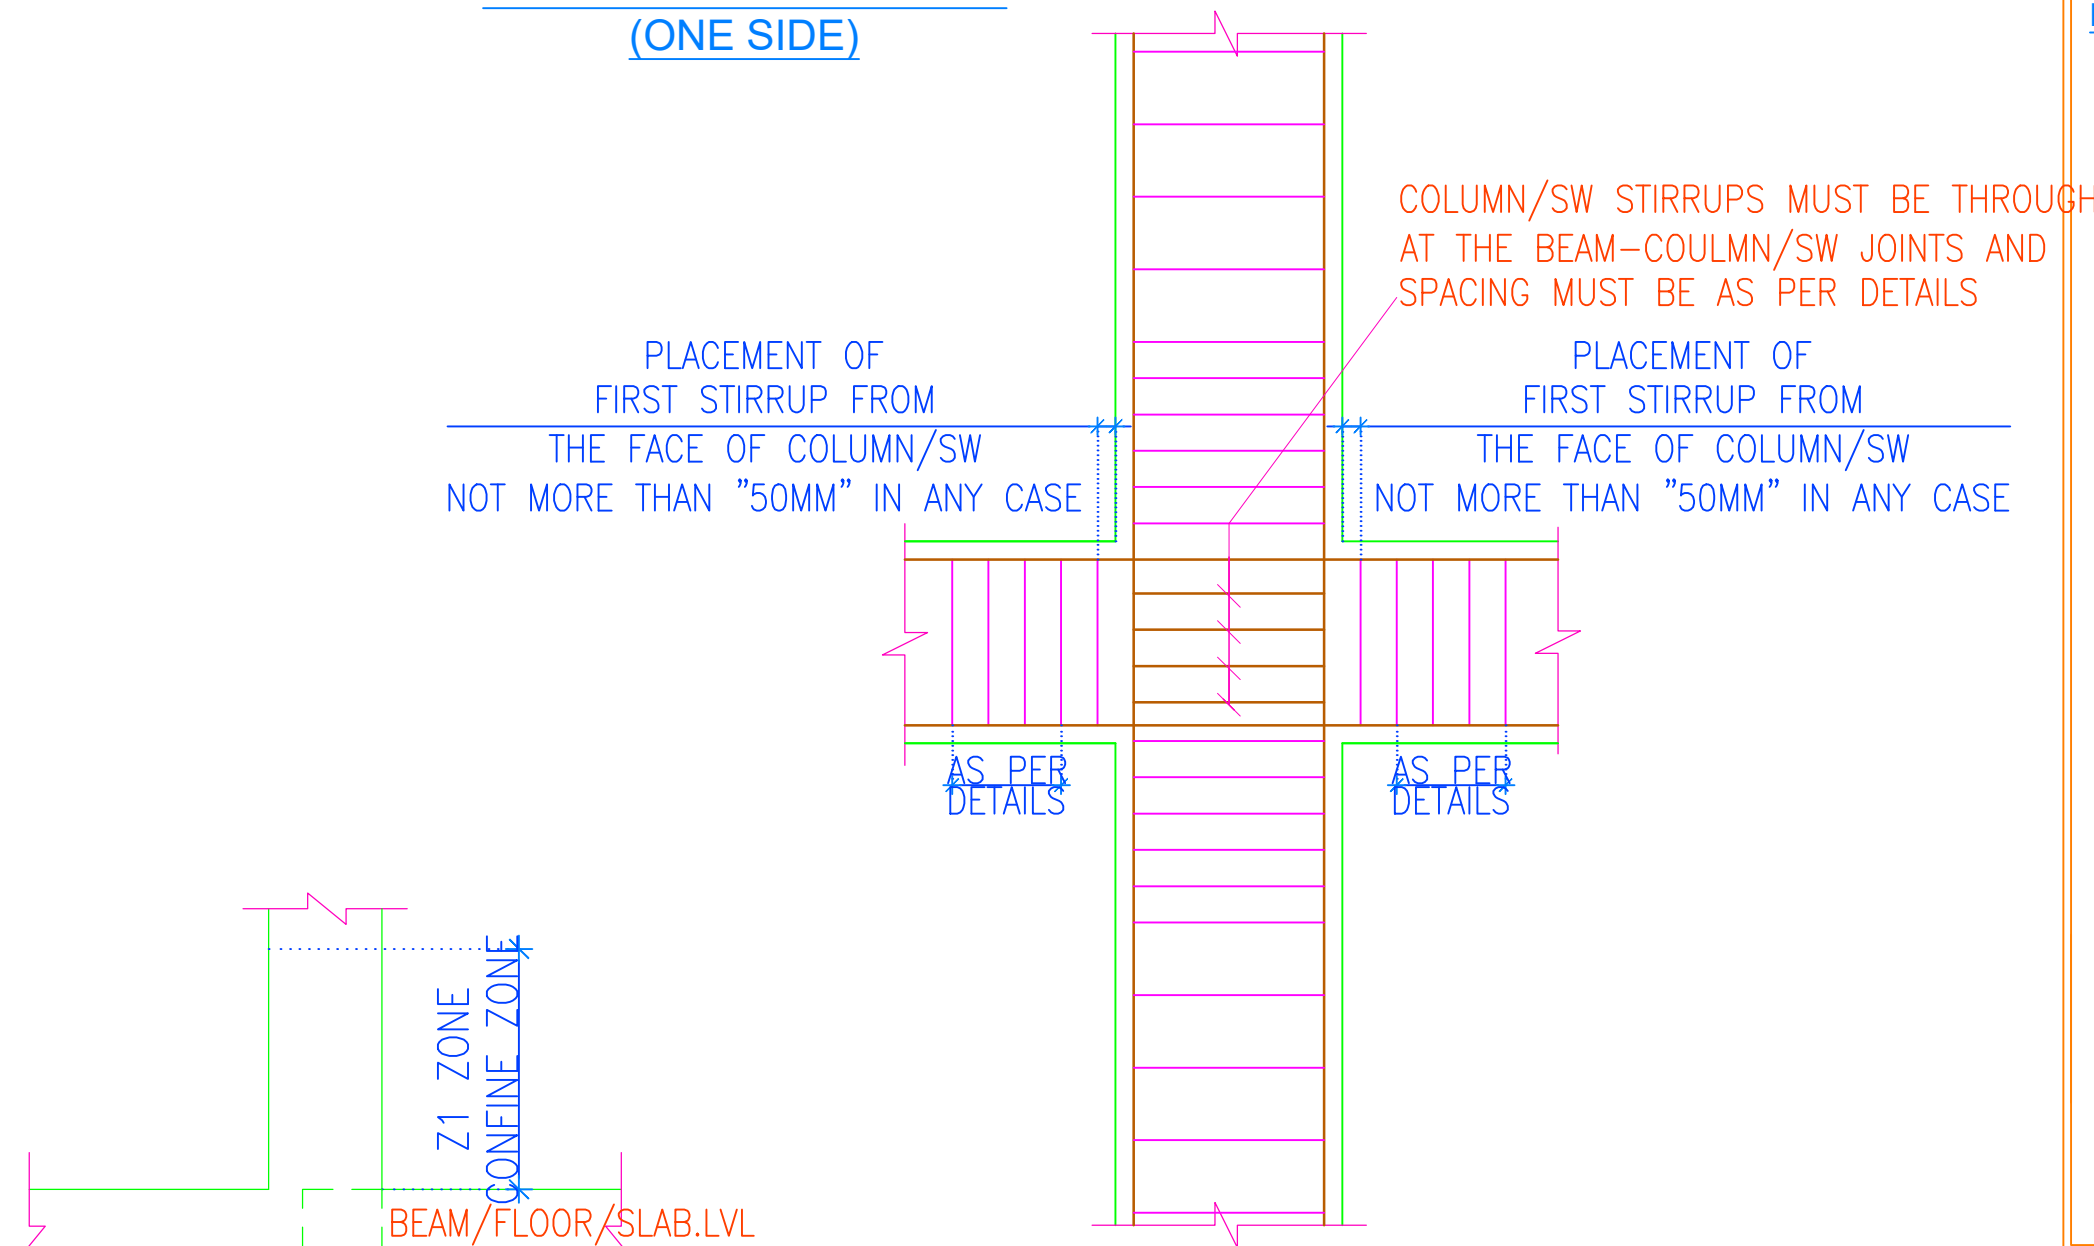


TYPICAL DETAILS FOR
STIRRUPS PLACEMENTS FOR
BEAMS AND COLUMNS

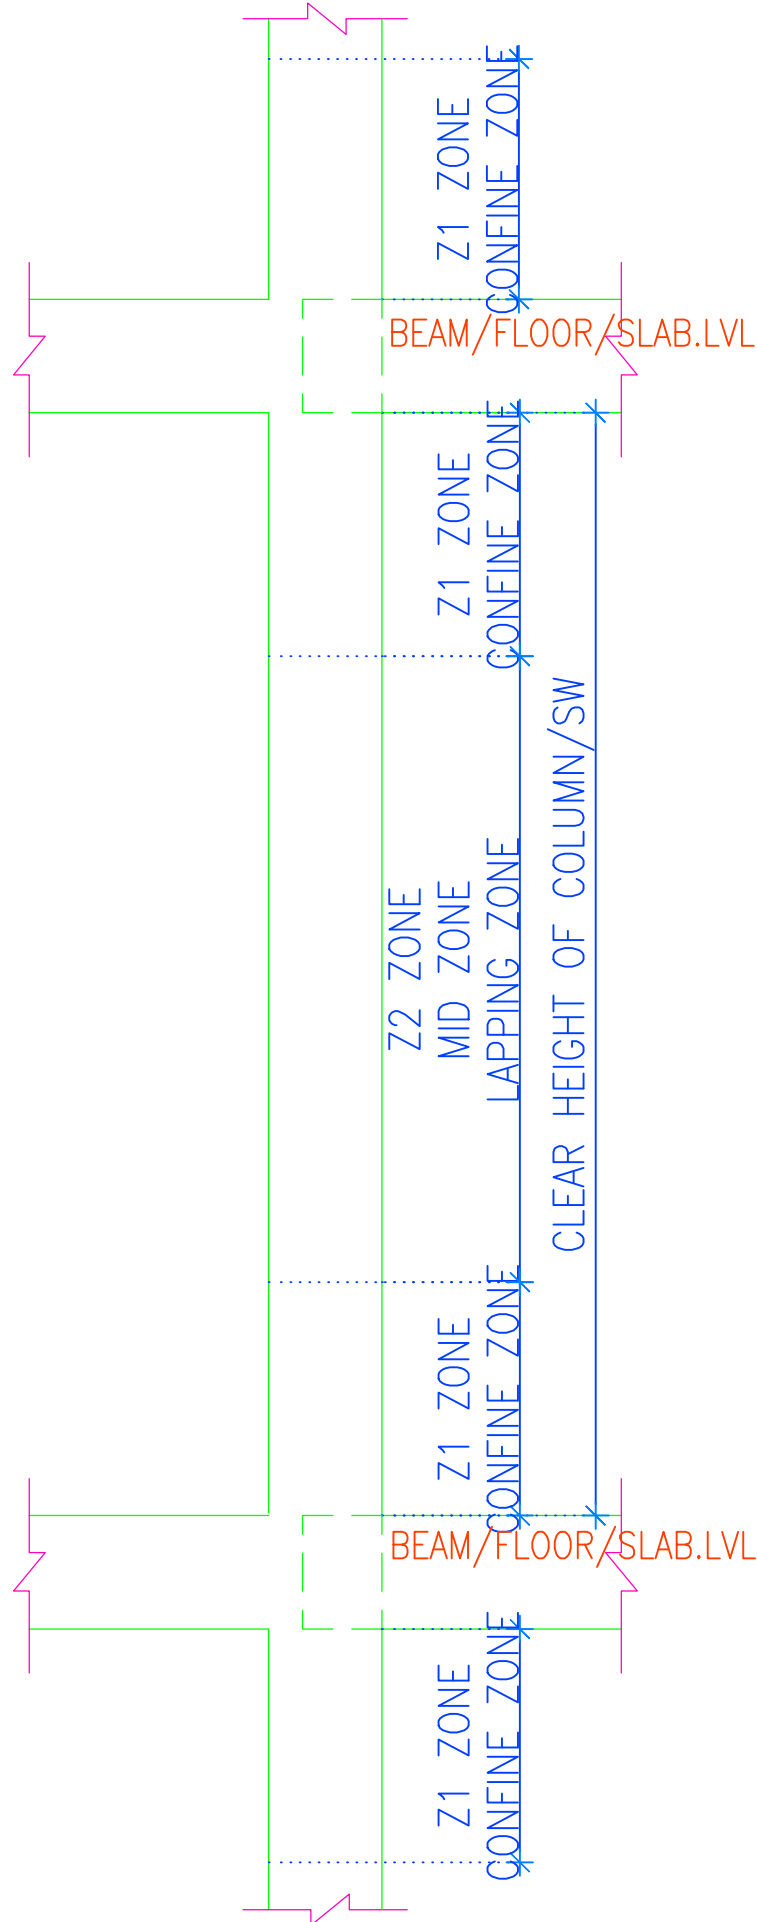

TYPICAL ZONING FOR
DUCTILE DETAILS
OF COLUMNS / SW

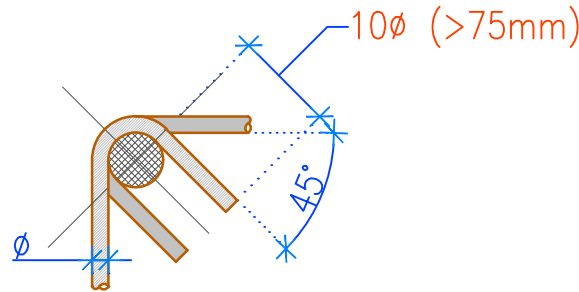

FOR 135° HOOK

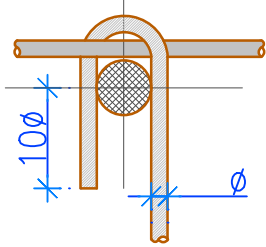

FOR 180° HOOK

TYPICAL DETAIL OF
HOOKS

GENERAL NOTES :-

1. ALL DIMENSIONS ARE IN MM.
2. FOR ALL NOTES, REFER OUR DRG NO: S0-01 TO S0-09.
3. CEMENT SHALL BE OPC 43 GRADE OR HIGHER / AS PER TENDER SPECIFICATIONS & PORTABLE WATER SHOULD BE USE.
4. SUPERVISION SHALL NOT BE OUR RESPONSIBILITY.
5. TO TAKE OUT THE CUBE AND MATERIAL TESTING SHALL BE CONTRACTOR/ BUILDER/CLIENTS RESPONSIBILITY.
6. LOAD TESTING OF STRUCTURE SHALL NOT BE OUR RESPONSIBILITY.
7. ALL DIMENSIONS ARE TO BE READ AND NOT TO BE MEASURED
8. T OR # INDICATE STEEL FE 500D GRADE TMT BARS.
9. ALL CONC.MIX. M:30 UNLESS OTHERWISE SPECIFIED.
10. L.D = DEVELOPMENT LENGTH : 50 X φ; WHERE, φ = DIA. OF BAR.
11. ALL BRICK WORK SHALL BE IN C.M. (1:6)
12. STRUCTURAL LAY OUT SHOULD BE REFER ONLY FOR STRUCTURAL DETAILING.
13. PLEASE REFER ARCHITECTURAL DWG FOR LVLS. & SETTINGS OUT CENTERLINE DIMENSIONS. THE CENTERLINE PUT IN THIS STRUCTURAL FOUNDATION LAYOUT IS SIMPLY INDICATIVE OF LOCATION AND AS APPROVED BY ARCHITECT.
14. PLEASE REFER ARCH. DWG. FOR FINAL LAY OUT.
15. CONTRACTOR SHOULD INFORM ARCHITECT/STRUCTURAL CONSULTANT IN CASE OF ANY CHANGE IN EXISTING CONDITION FOUND, IMMEDIATELY
16. THIS DRG. SHOULD BE READ ALONG WITH ARCHITECTURAL DRGS. AND ANY CHANGES/DEVIATION FOUND SHOULD BE IMMEDIATELY BROUGHT TO NOTICE OF ARCHITECT & STR. ENGINEER
17. THIS DWG. SHOULD BE READ ALONG WITH RELEVANT DETAILS
18. MIX DESIGN SHOULD BE GOT APPROVED PRIOR TO EXECUTION OF WORK
19. ALL STEEL (TOP/BOTTOM) OF DIFFERENT ZONE SHALL BE LAPPED IN ADDITION WHERE THE ZONE TERMINATES; BY LENGTH EQUAL TO THE DEVELOPMENT LENGTH OF HIGHER DIA BAR.

KEY PLAN




GRADE OF CONCRETE

ALL STRUCTURAL ELEMENTS	M30
-------------------------	-----

CONCRETE COVER

FOOTINGS /RAFT	50MM
COLUMNS/SW	40MM
BEAMS	30MM
SLABS	25MM
PARDI WALLS	30MM

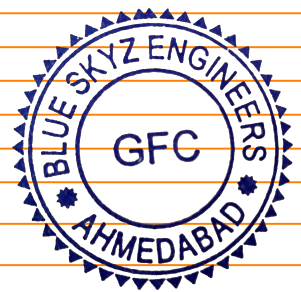

1	29-12-21	GOOD FOR CONSTRUCTION		
---	----------	-----------------------	--	--

NO.	DATE	REVISION / REMARK	BY	DR	CH
-----	------	-------------------	----	----	----

JOB TITLE / DEVELOPER

TURQUOISE-GRANDEUR
RATANA DEVELOPERS

DRAWING TITLE

COLUMN SCHEDULE DETAIL - TOWER-A

JOB NO 2111		DATE 16/04/2021		DRG. NO. S5-TA-07		REVISION R0			
SCALE 1 : 100		SHEET SIZE A1/A2/A3		DRAWN AKSHAY		DESIGN KUNJ		CHECKED BHAVIK PATEL	

ARCHITECTS



HM ARCHITECTS
e:contact@hmarchitects.in

STRUCTURAL CONSULTANT



email: blueskyzengineers@gmail.com