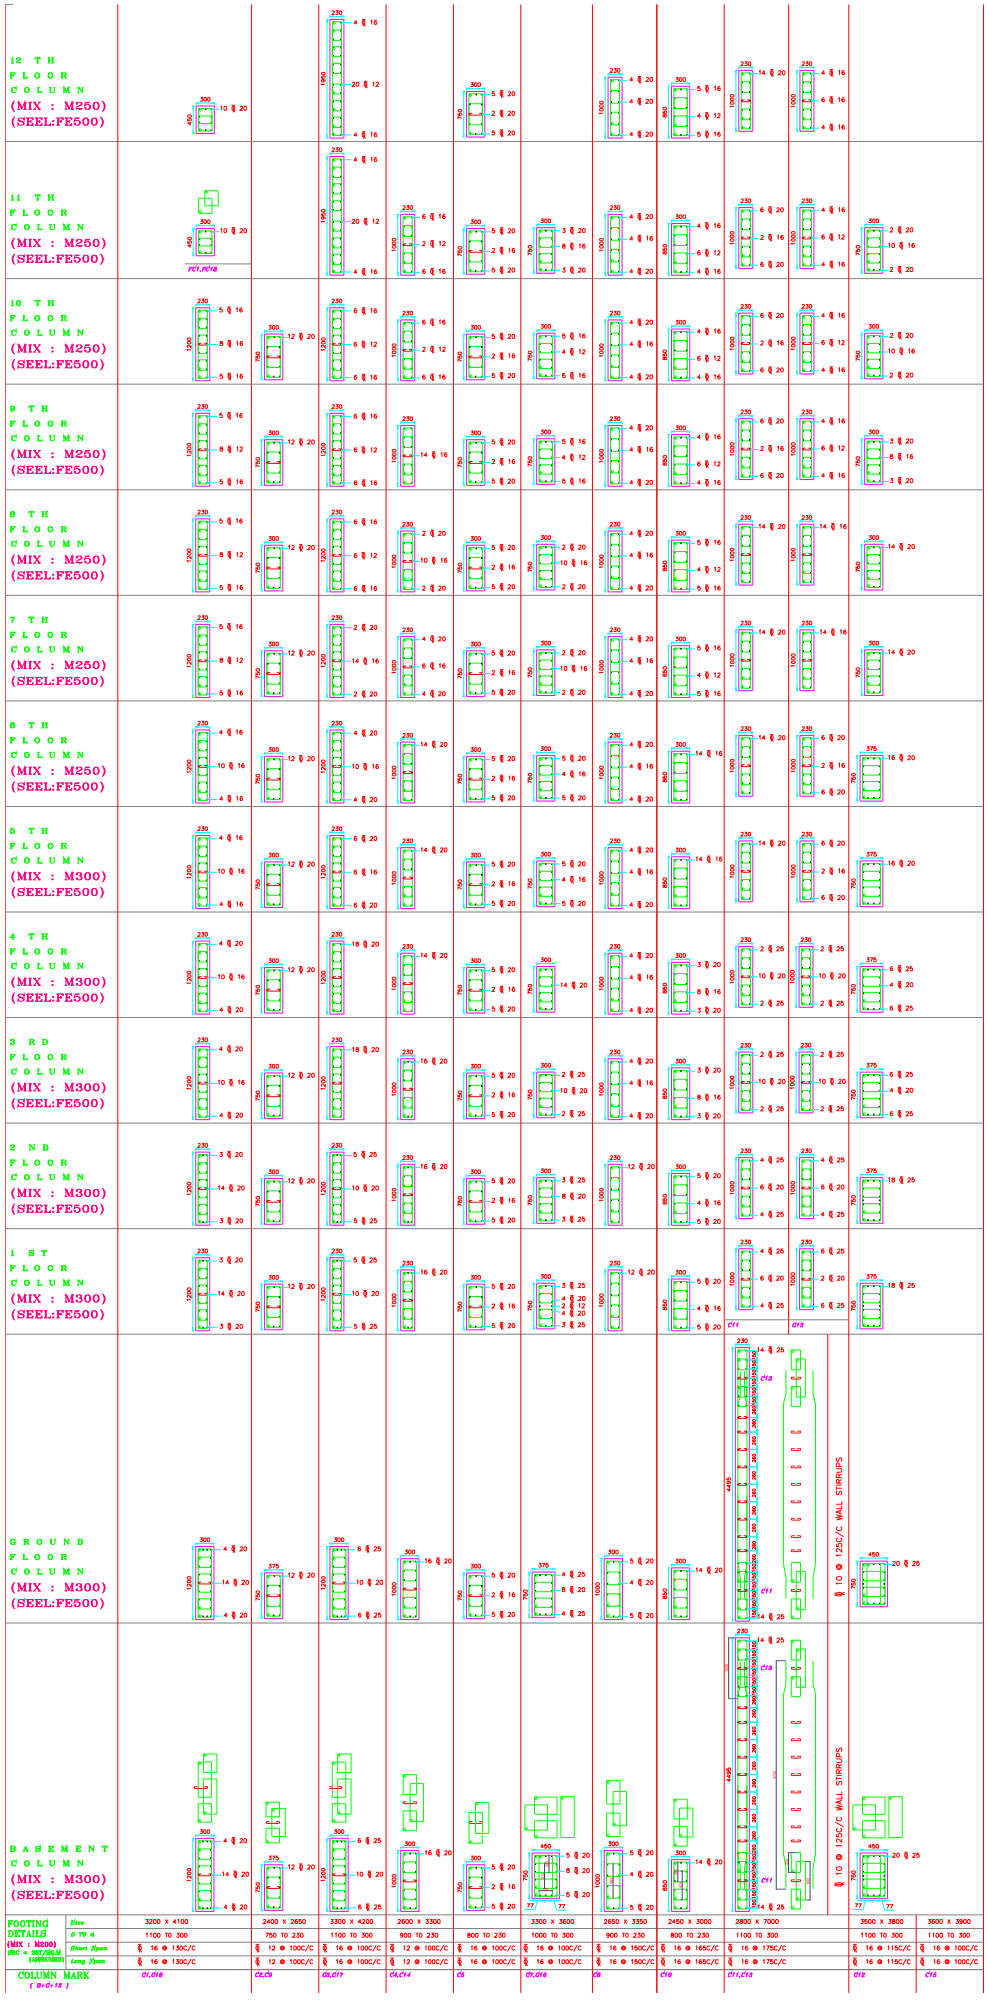
12 TH FLOOR COLUMN (MIX : M250) (SEEL:FE500)
11 TH FLOOR COLUMN (MIX : M250) (SEEL:FE500)
10 TH FLOOR COLUMN (MIX : M250) (SEEL:FE500)
9 TH FLOOR COLUMN (MIX : M250) (SEEL:FE500)
8 TH FLOOR COLUMN (MIX : M250) (SEEL:FE500)
7 TH FLOOR COLUMN (MIX : M250) (SEEL:FE500)
6 TH FLOOR COLUMN (MIX : M250) (SEEL:FE500)
5 TH FLOOR COLUMN (MIX : M300) (SEEL:FE500)
4 TH FLOOR COLUMN (MIX : M300) (SEEL:FE500)
3 RD FLOOR COLUMN (MIX : M300) (SEEL:FE500)
2 ND FLOOR COLUMN (MIX : M300) (SEEL:FE500)
1 ST FLOOR COLUMN (MIX : M300) (SEEL:FE500)
GROUND FLOOR COLUMN (MIX : M300) (SEEL:FE500)
BASEMENT COLUMN (MIX : M300) (SEEL:FE500)
C11
C13
4445
@ 10 @ 125C/C WALL STIRRUPS
FOOTING DETAILS
Size
D TO d
(MIX : M300) (BC = 25T/SQ.M (ASSUMED))
Short Span
Long Span
COLUMN MARK (B+G+12)
3200 X 4100
2400 X 2650
3300 X 4200
2600 X 3300
3300 X 3600
2650 X 3350
2450 X 3000
2800 X 7000
3500 X 3800
3600 X 3900
1100 TO 300
750 TO 250
900 TO 250
800 TO 250
1000 TO 500
C1,C18
C12,C9
C3,C17
C4,C14
C5
C7,C16
C8
C10
C11,C13
C12
C15